

WALL LEGEND

-  = EXISTING WALL
-  = NEW 2x WOOD FRAME @ 16" O.C. WALL w/ 1/2" GYPBOARD ON EITHER SIDE
-  = EXISTING WALL TO BE DEMOLISHED

CONSTRUCTION LEGEND

1. DO NOT SCALE DRAWINGS.
2. ALL DIMENSIONS SHALL BE FIELD VERIFIED AND ANY DISCREPANCIES SHALL BE REPORTED PRIOR TO COMMENCEMENT OF WORK.
3. REFER TO GENERAL NOTES FOR ADDITIONAL INFORMATION.

GENERAL NOTES

NOTE 1:
KITCHEN, PANTRY, & POWDER ROOM FINAL CABINETRY TO BE DESIGNED BY INTERIOR DESIGNER / CABINET MAKER. VERIFY w/ CABINET MAKER'S PLANS.

NOTE 2:
UPON COMPLETION OF THE KITCHEN DESIGN, CONTRACTOR SHALL RETURN UPDATED PLANS TO THE ARCHITECT FOR ELECTRICAL COORDINATION AND REVISIONS.

NOTE 3:
REMOVE EXISTING PLASTER AND GUT WALLS DOWN TO STUDS. PROVIDE NEW SISTER STUDS AND JOISTS ADJACENT TO EXISTING FRAMING AS REQUIRED TO ACHIEVE PLUMB, FLAT AND TRUE CONDITIONS AT ALL CABINET INSTALLATION SURFACES, INCLUDING FLOORS, WALLS AND CEILINGS.

NOTE 4: CONTRACTOR TO VERIFY THERE IS ENOUGH SPACE FOR 6" ABOVE THE KITCHEN COUNTER FOR BACKSPLASH & HORIZONTAL OUTLETS. (PRADO OUTLETS RECOMMENDED. REFERENCE PHOTO BELOW)




SCHEMATIC 3D VIEW - ISO



SCHEMATIC 3D VIEW - KITCHEN




SCHEMATIC 3D VIEW - KITCHEN

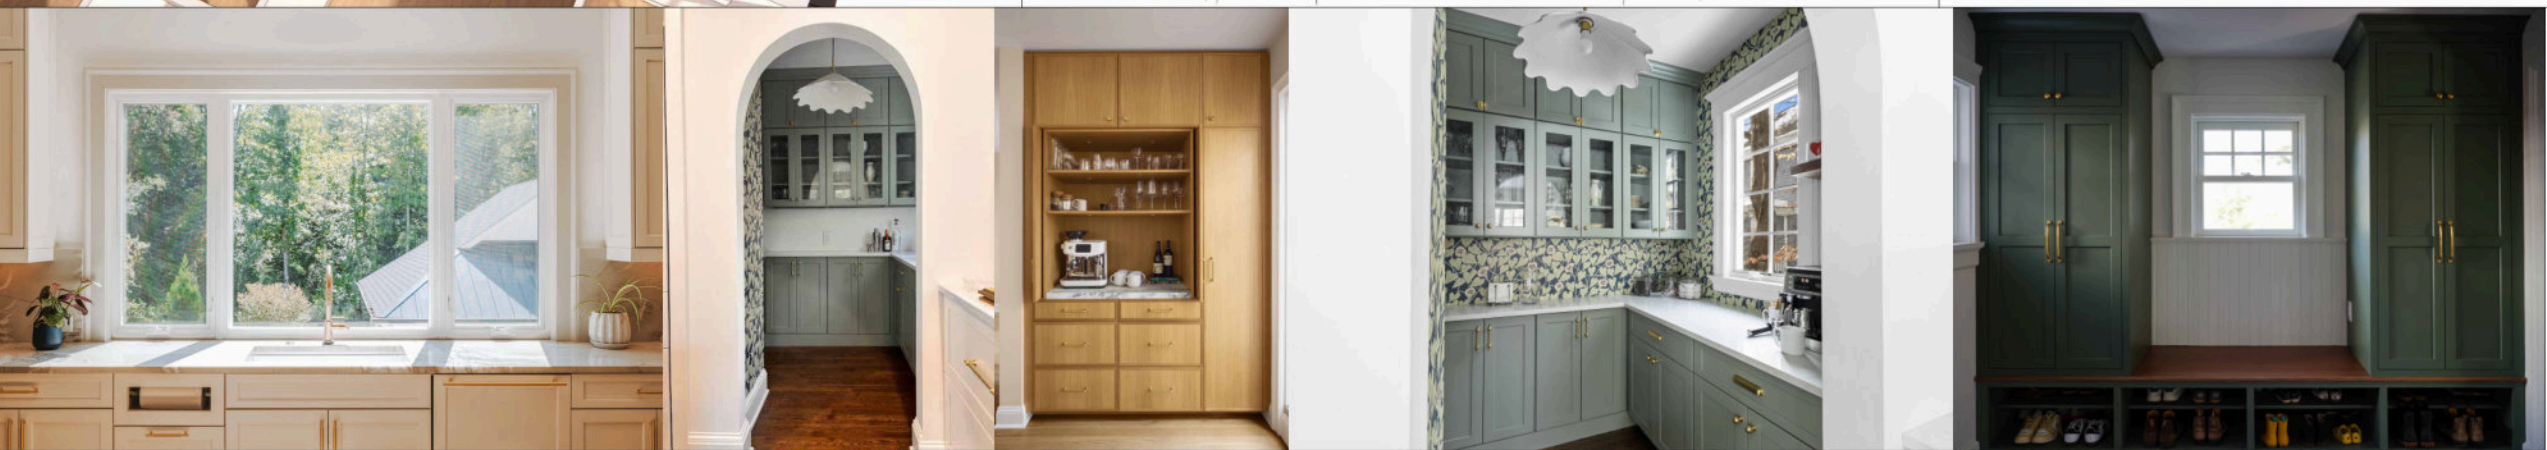

INSPO PHOTOS

REMODEL EXISTING KITCHEN, REMOVE EXISTING CABINETS / STORAGE, APPLIANCES, LIGHT FIXTURES, PLUMBING FIXTURES AND ALL ASSOCIATED COMPONENTS

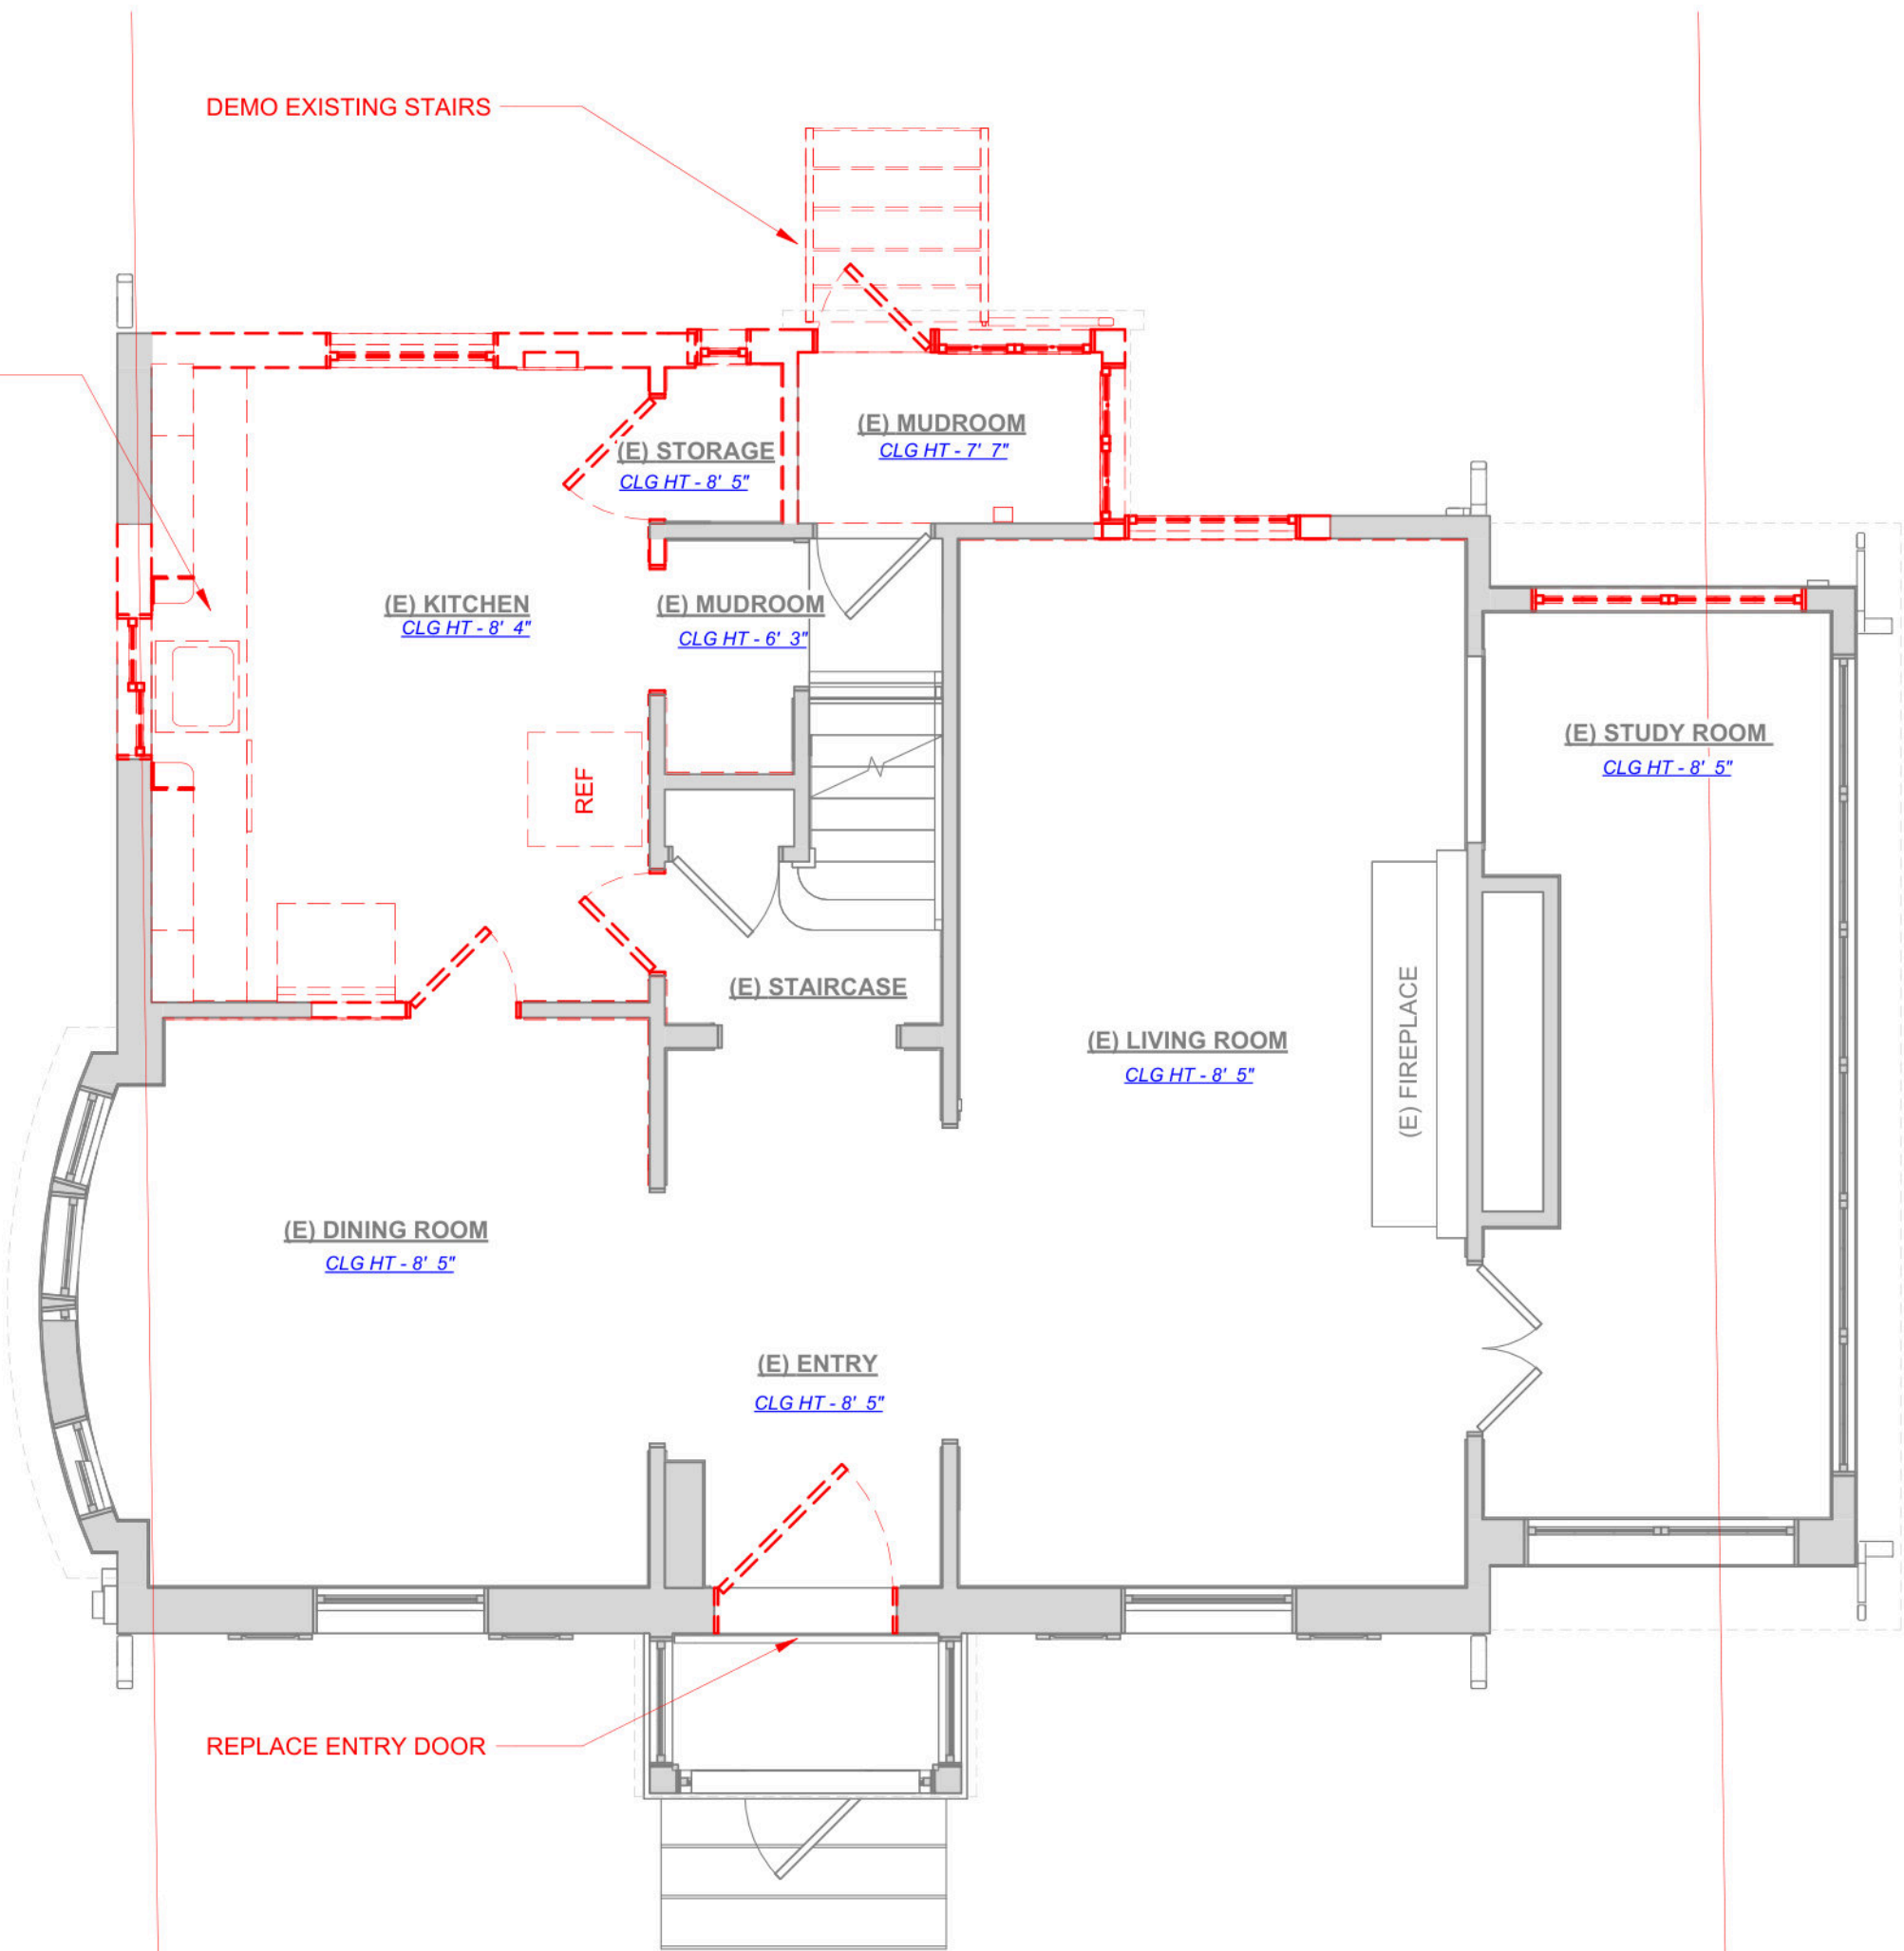


1 Existing - First Floor
1/4" = 1'-0"

CONTRACTOR TO VERIFY THERE IS MIN. 6" SPACE ABOVE THE KITCHEN COUNTER FOR HORIZONTAL OUTLETS

HOOD VENTILATION TO EXTERIOR. INSTALL MAKE UP AIR DAMPER IF HOOD IS OVER 400 CFM

FINAL CABINETRY TO BE DESIGNED BY INTERIOR DESIGNER - VERIFY w/ CABINET MAKER'S PLANS.

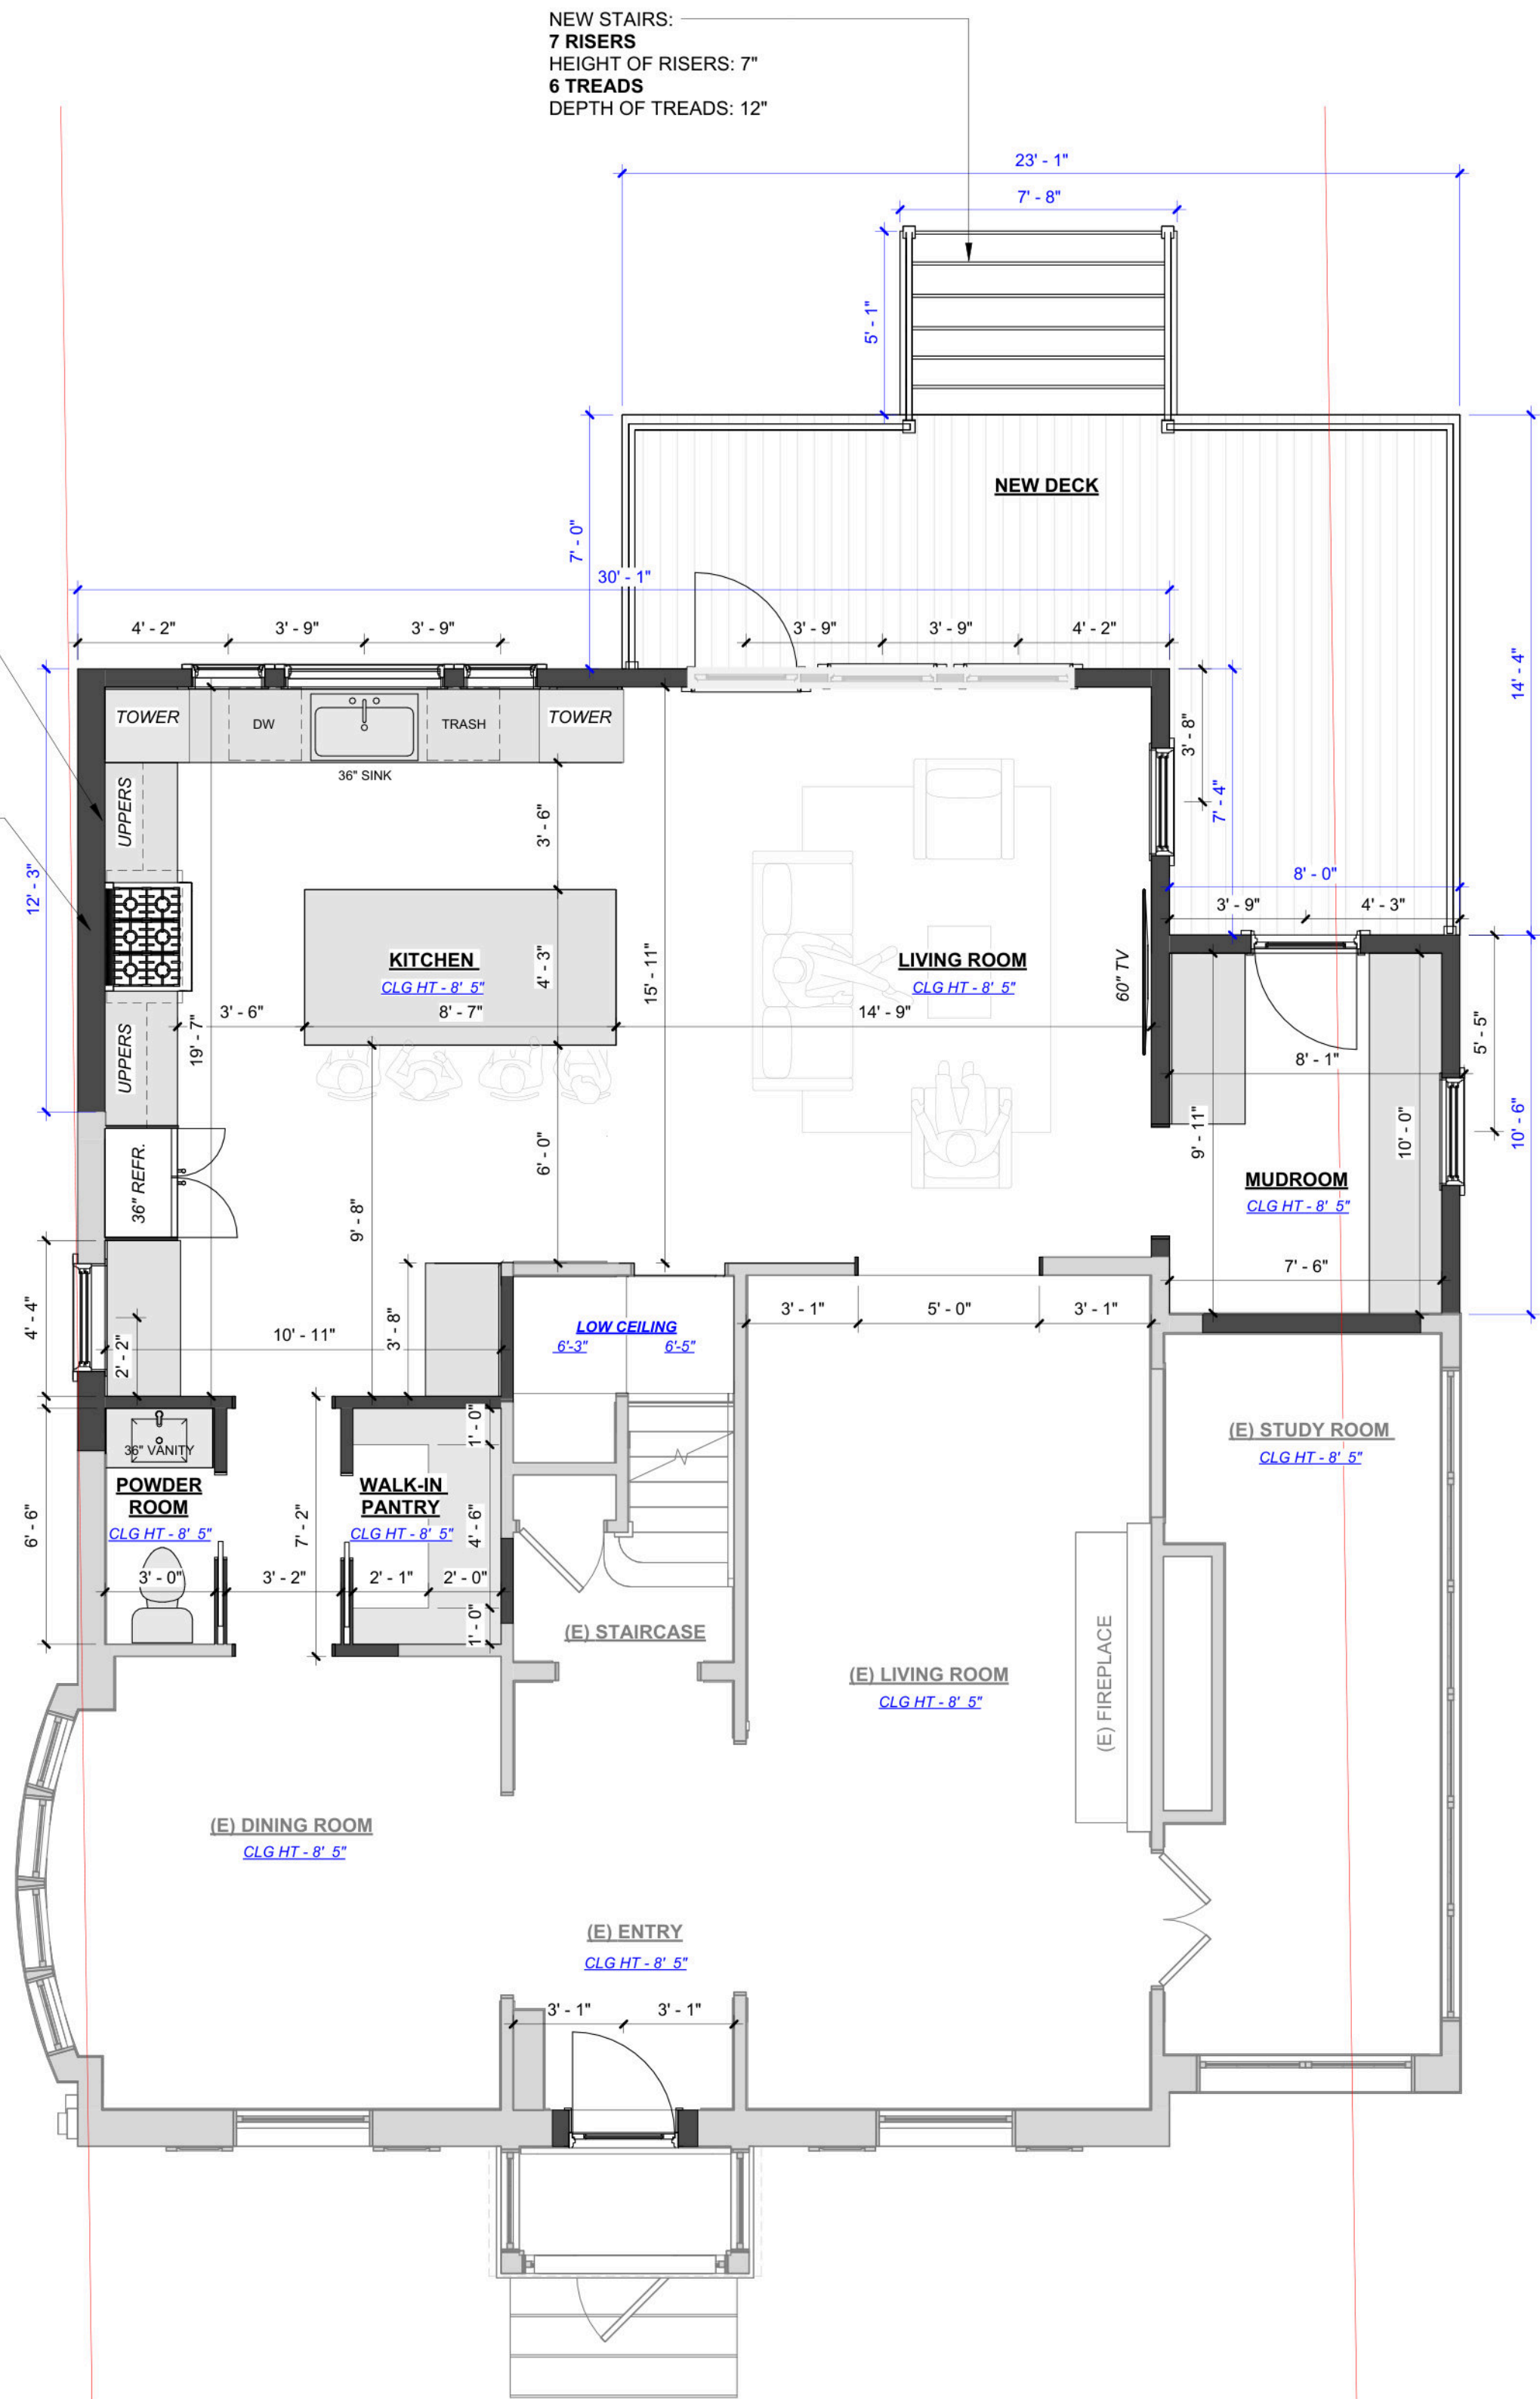

2 Proposed - First Floor.
1/4" = 1'-0"

REVISIONS	BY

Courtney Rombough A.I.A. LLC

ARCHITECT

ARCHITECT'S ADDRESS : 141 Central Ave., Montclair, NJ
PHONE: 973.985.8230
WEBSITE: COURTNEYROMBOUGH.COM
EMAIL: COURTNEY@COURNEYROMBOUGH.COM

COURTNEY ROMBOUGH A.I.A. LLC
RA #21A02047700
08.13.2026

GARRIGAN JULIA & JACK

261 GROOVE STREET
MONTCLAIR, NEW JERSEY 07042
BLOCK 4512 - LOT 22

DRAWN	CHECKED
DATE	08.13.2026
SCALE	1/4" = 1'-0"
JOB	
DWG	
SHEET	

A-1