

WALL LEGEND

-  = EXISTING WALL
-  = NEW 2x WOOD FRAME @ 16" O.C. WALL w/ 1/2" GYPBOARD ON EITHER SIDE
-  = EXISTING WALL TO BE DEMOLISHED

CONSTRUCTION LEGEND




- DO NOT SCALE DRAWINGS.
- ALL DIMENSIONS SHALL BE FIELD VERIFIED AND ANY DISCREPANCIES SHALL BE REPORTED PRIOR TO COMMENCEMENT OF WORK.
- REFER TO GENERAL NOTES FOR ADDITIONAL INFORMATION.

GENERAL NOTES

1. FRAMING NOTE – CMU OPENING
AT NEW DOOR OPENING, CUT CMU WALL FULL HEIGHT AS REQUIRED. PROVIDE REINFORCEMENT OF WOOD FRAMING ABOVE OPENING TO MEET APPLICABLE NEW JERSEY BUILDING CODE REQUIREMENTS. CONTRACTOR TO VERIFY EXISTING CONDITIONS AND PROVIDE FRAMING AS REQUIRED FOR CODE COMPLIANCE.


2. EXISTING CEILING AND FLOORS
REMOVE [E] UNNECESSARY PIPING + WIRING FROM CLG THROUGHOUT BASEMENT. REPLACE w/ SHEETROCK CLG (AS HIGH AS POSSIBLE) w/ RECESSED LIGHTS. INSTALL [N] WOOD OR TILE FLOORS IN ALL ROOMS. IF FLOOR IS DAMP, USE DRICORE SUBFLOOR TO ISOLATE THE FLOOR FINISH FROM THE DAMP SLAB.

3. CMU WALLS FINISH
VERIFY WALLS ARE DRY BEFORE APPLYING FINISHES. ADD VAPOR BARRIER + RIGID FOAM INSULATION FOLLOWED BY STUD FRAME + DRYWALL. USE PRESSURE TREATED OR STEEL BOTTOM PLATE. STAND FRAMING OFF WALL 1". USE PVC BASEBOARD. FRAMING TO BE #2 GROUND CONTACT PTL.

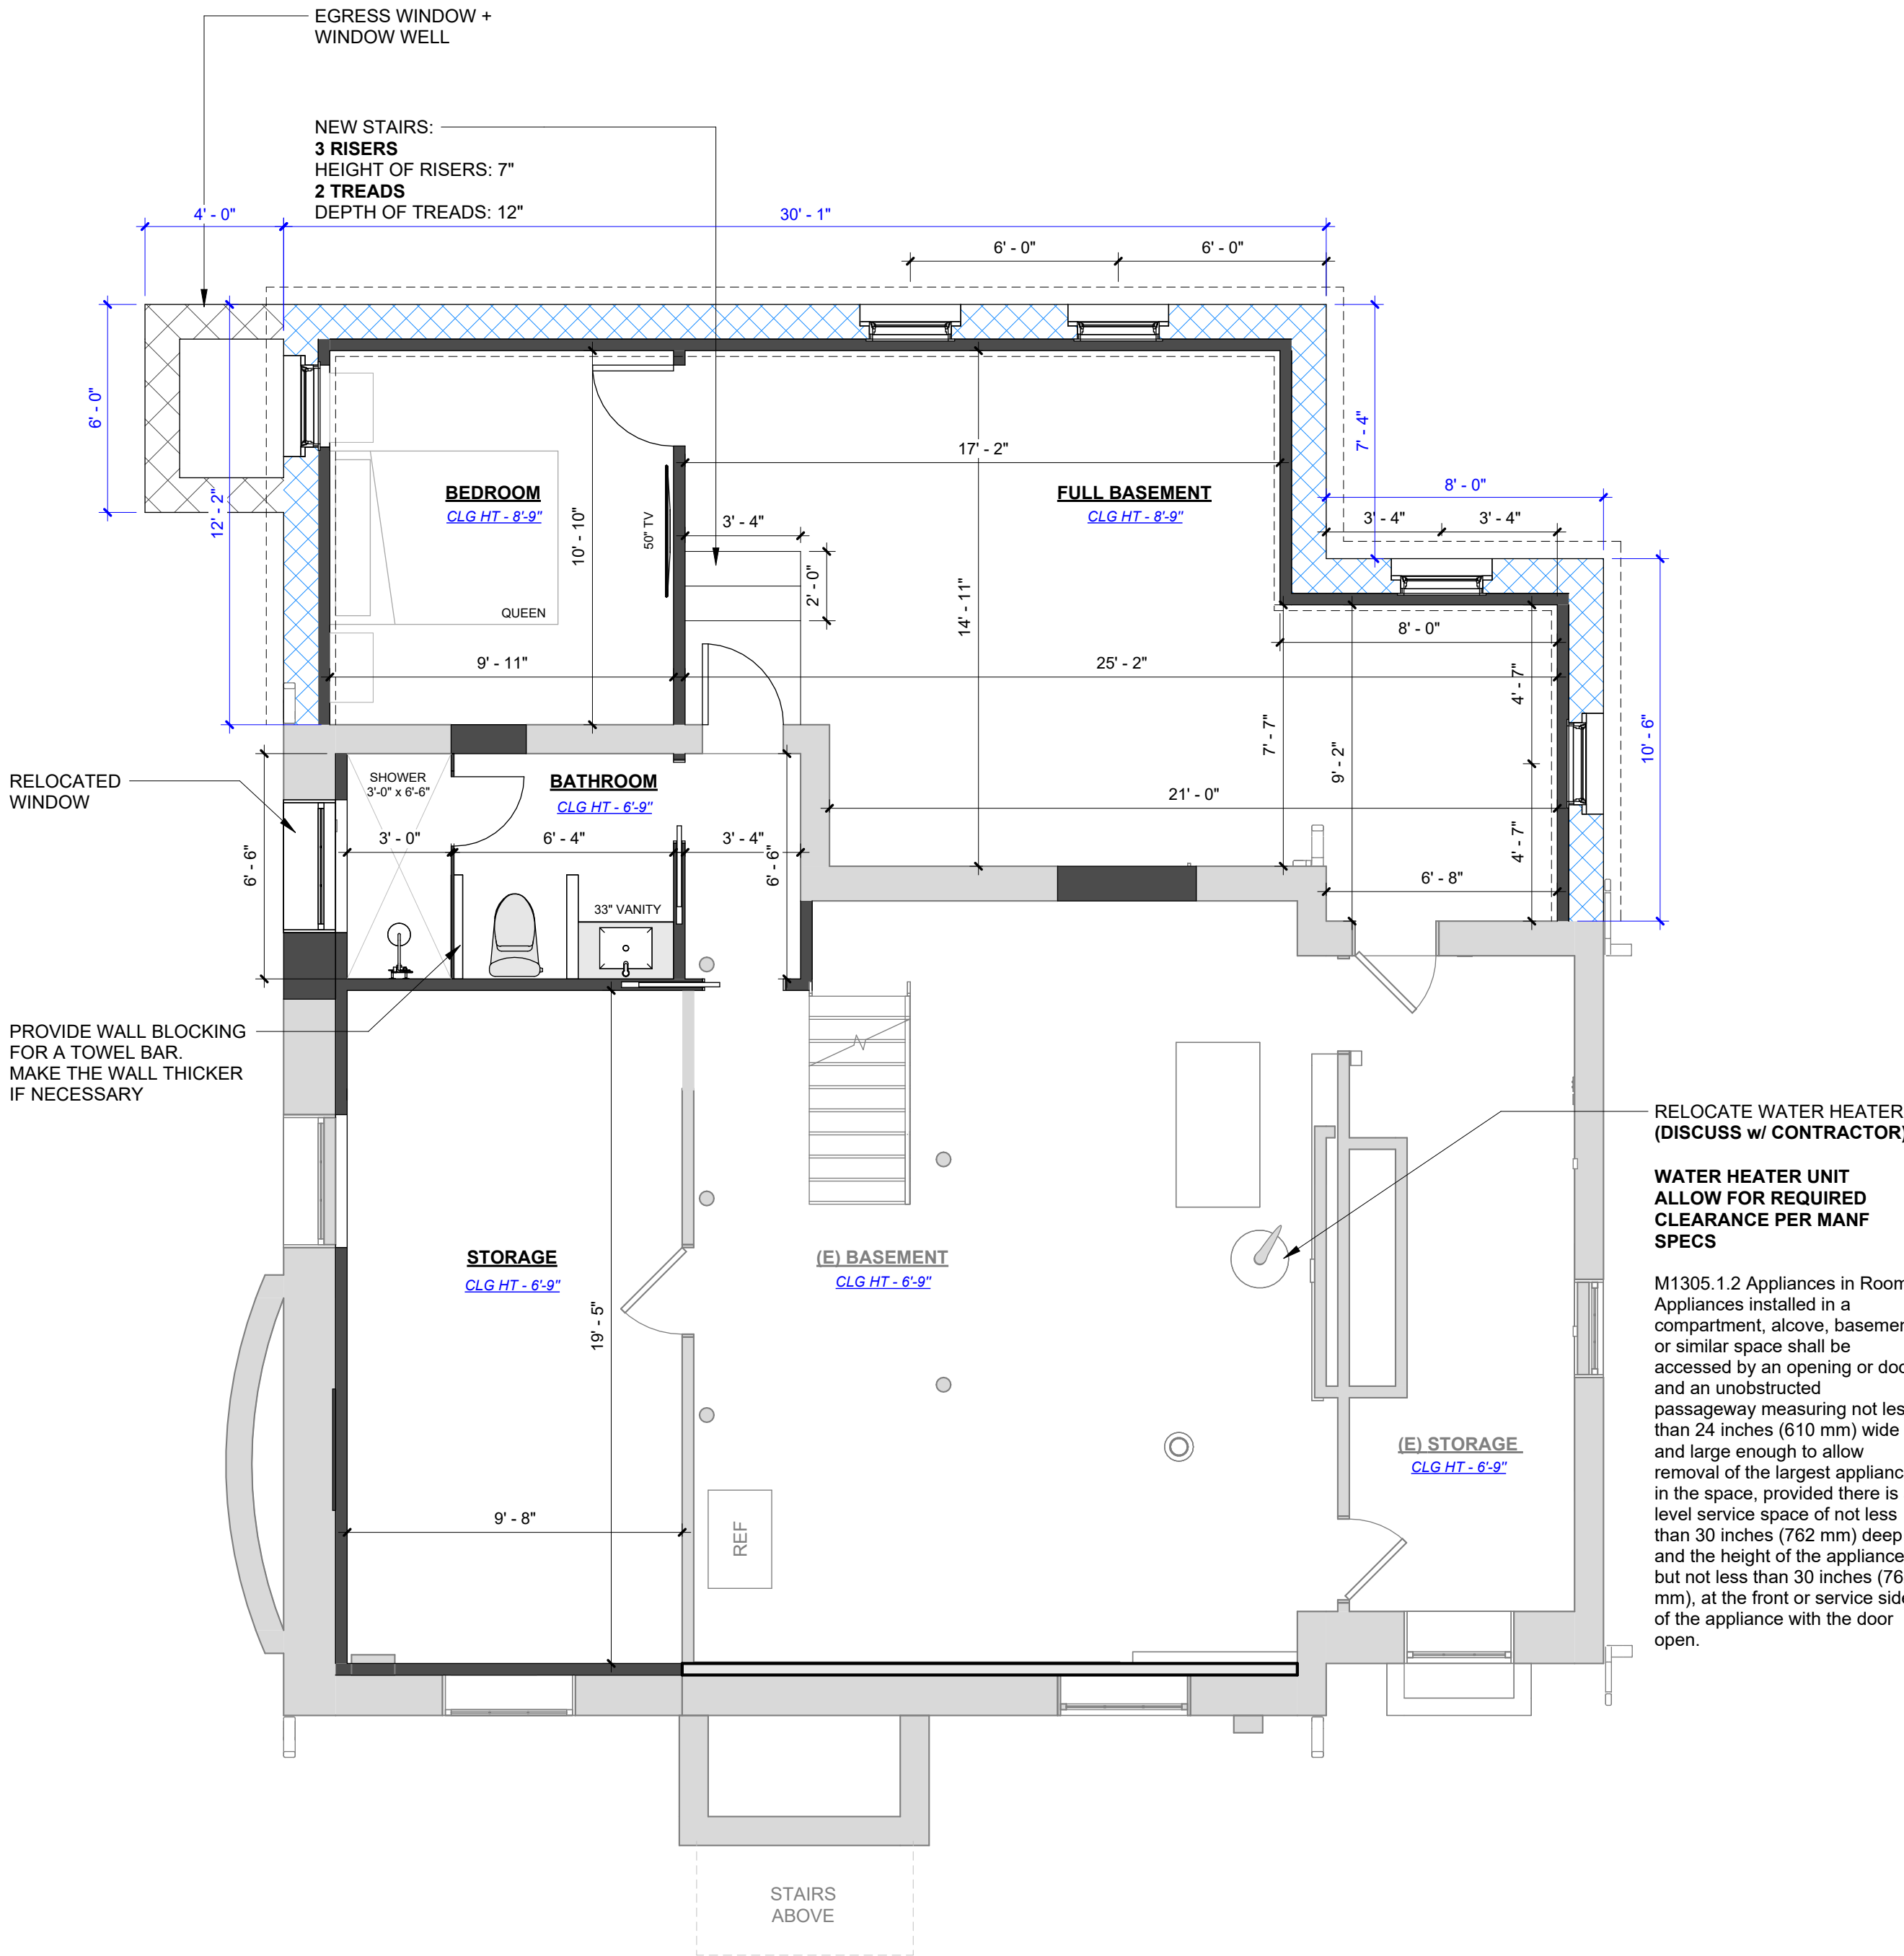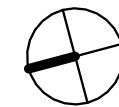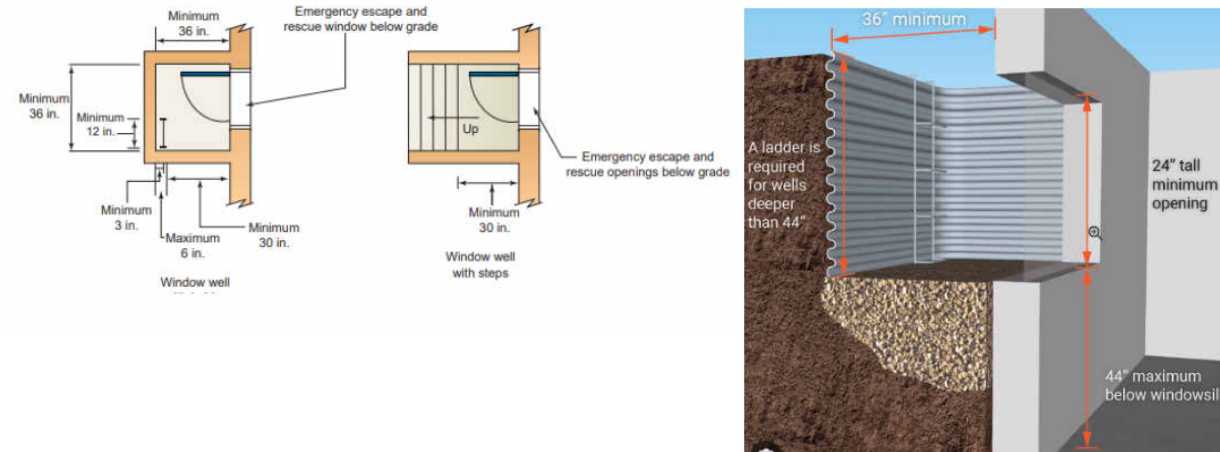

② Proposed - Basement Floor.
1/4" = 1'-0"

DEMO EXISTING BATHROOM, REMOVE EXISTING VANITY, APPLIANCE, LIGHT FIXTURES, PLUMBING FIXTURES AND ALL ASSOCIATED COMPONENTS

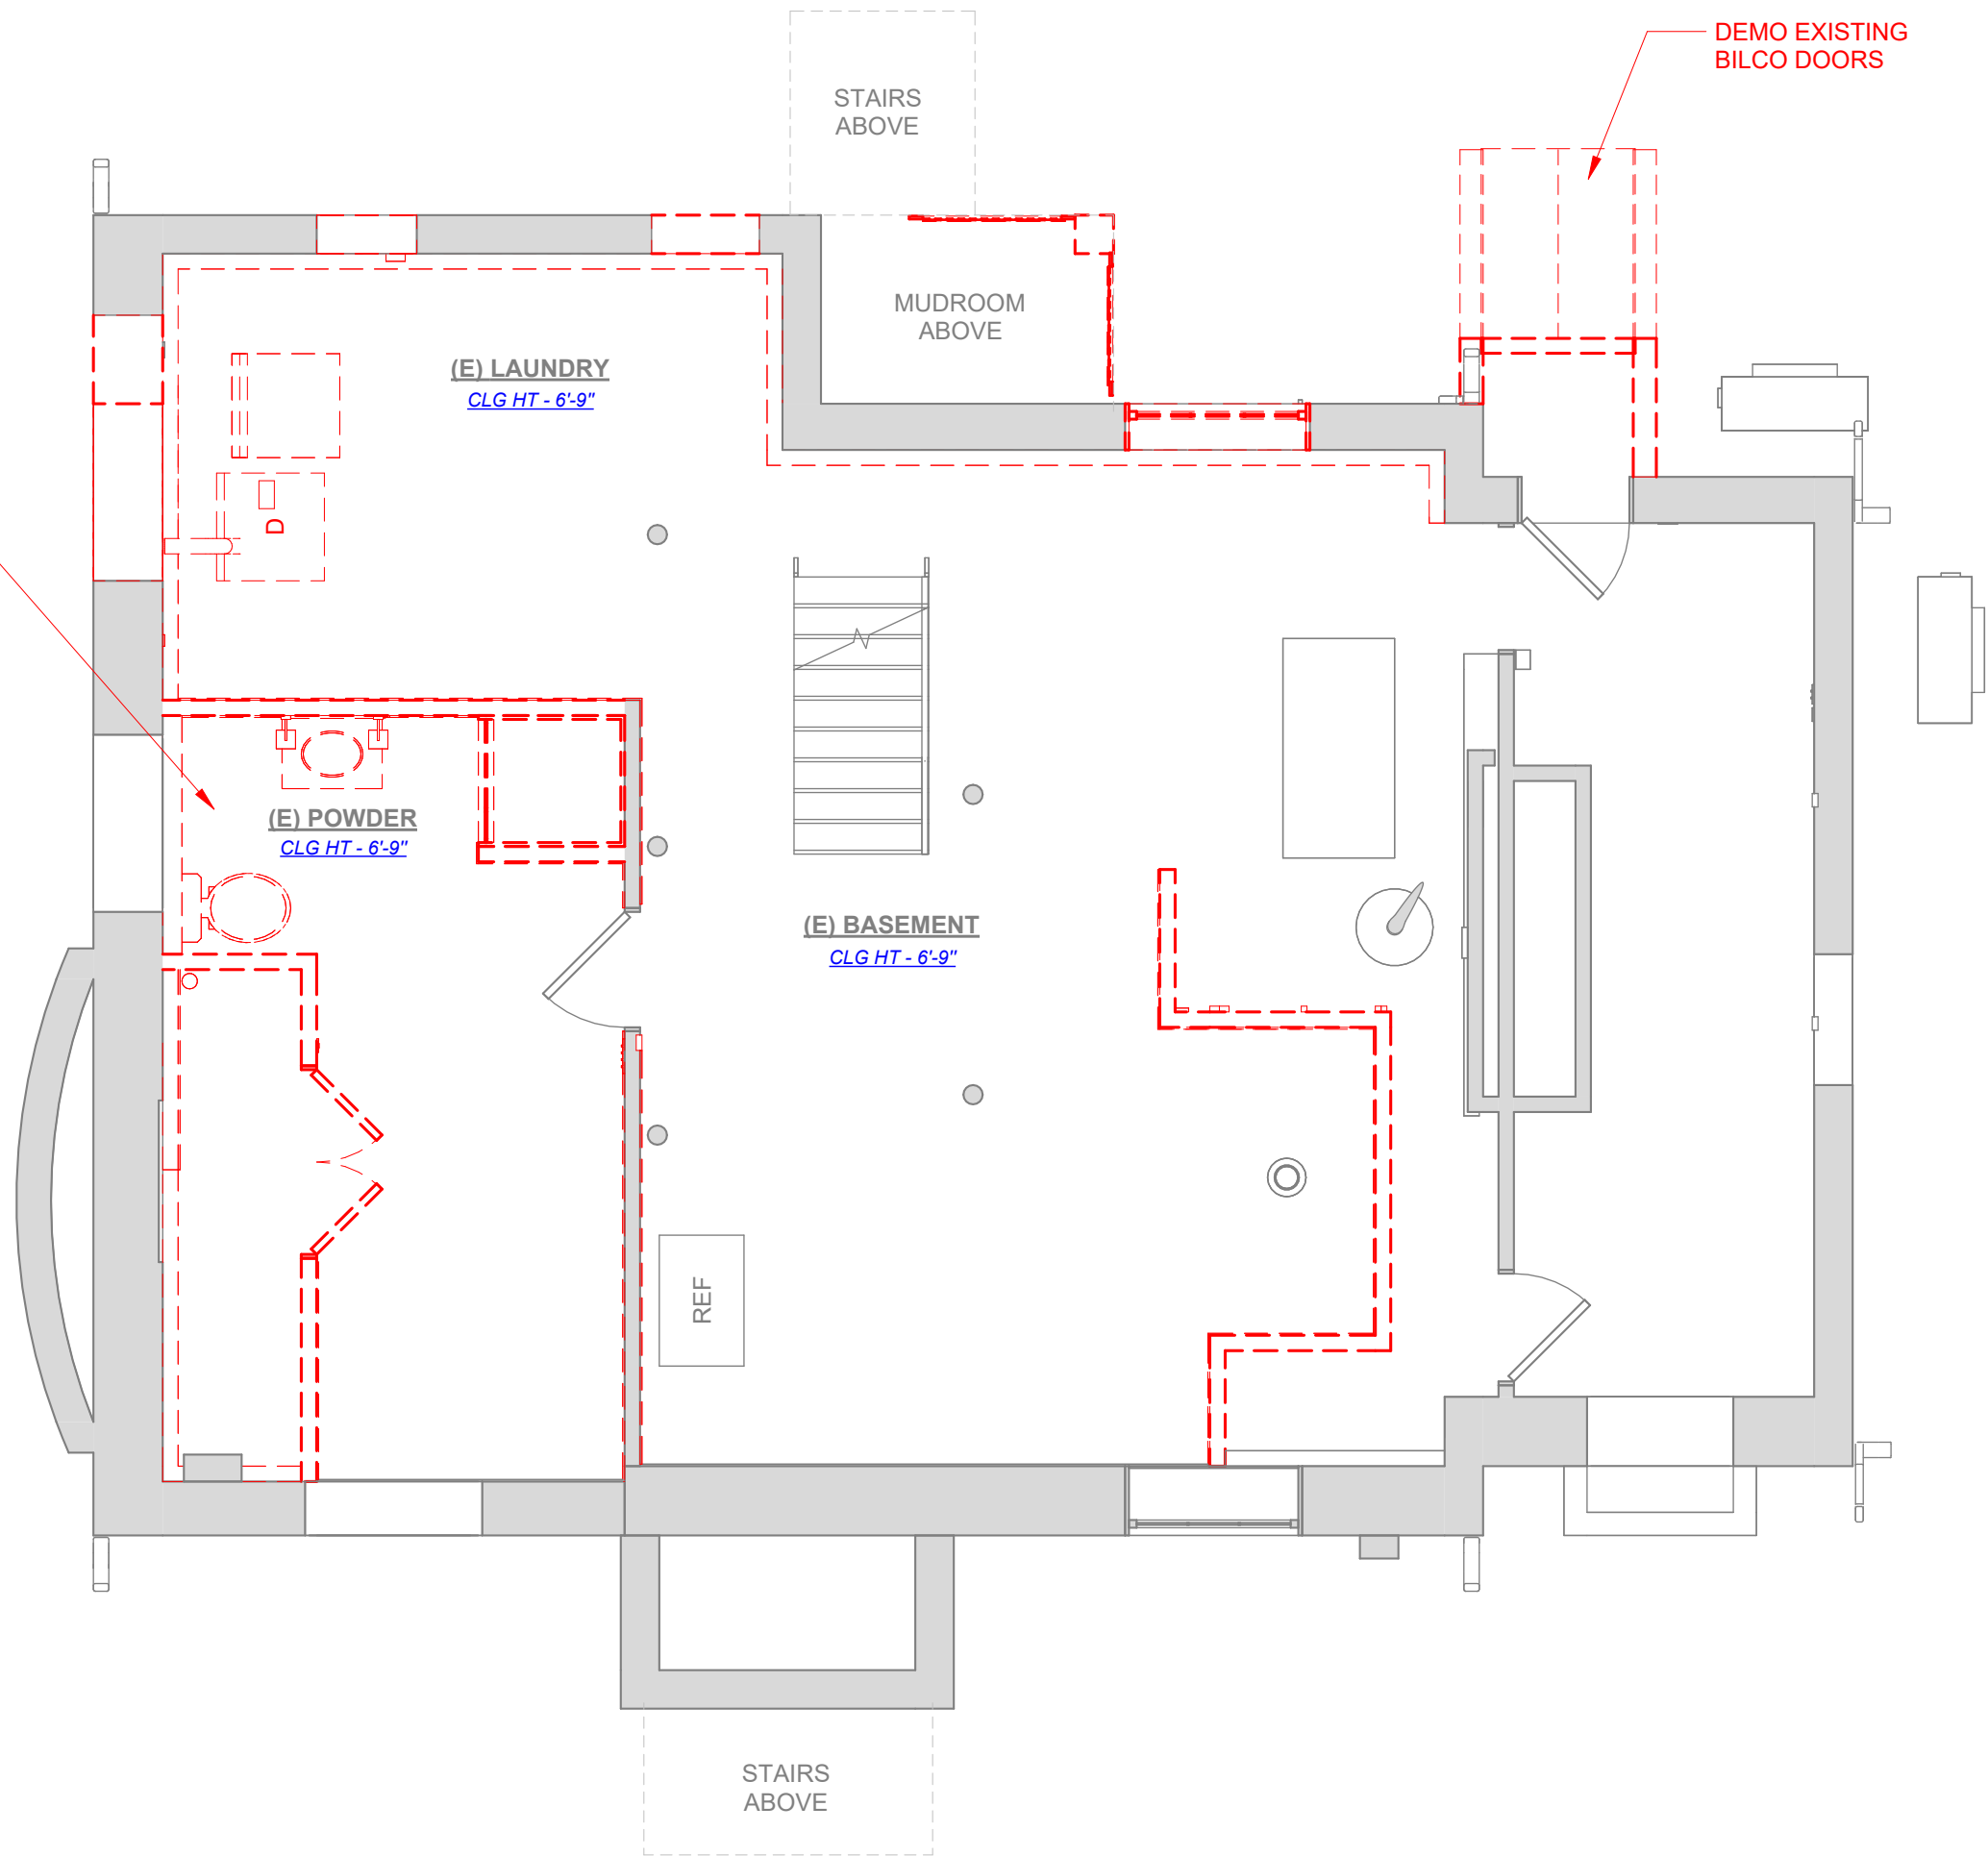

① Existing - Basement Floor.
1/4" = 1'-0"

REVISIONS	BY

Courtney Rombough A.I.A. LLC
ARCHITECT

ARCHITECT'S ADDRESS: 141 Central Ave. Montclair, NJ
PHONE: 973.985.8230
WEBSITE: COURTNEYROMBOUGH.COM
EMAIL: COURTNEY@COURTNEYROMBOUGH.COM

COURTNEY ROMBOUGH A.I.A. LLC
RA #21A02047700
08.13.2026

GARRIGAN JULIA & JACK

261 GROOVE STREET
MONTCLAIR, NEW JERSEY 07042
BLOCK 4512 - LOT 22

DRAWN	CHECKED
DATE	08.13.2026
SCALE	As indicated
JOB	
DWG	
SHEET	

A-0

WALL LEGEND

-  = EXISTING WALL
-  = NEW 2x WOOD FRAME @ 16" O.C. WALL w/ 1/2" GYPBOARD ON EITHER SIDE
-  = EXISTING WALL TO BE DEMOLISHED

CONSTRUCTION LEGEND

1. DO NOT SCALE DRAWINGS.
2. ALL DIMENSIONS SHALL BE FIELD VERIFIED AND ANY DISCREPANCIES SHALL BE REPORTED PRIOR TO COMMENCEMENT OF WORK.
3. REFER TO GENERAL NOTES FOR ADDITIONAL INFORMATION.

GENERAL NOTES

- NOTE 1:** KITCHEN, PANTRY, & POWDER ROOM FINAL CABINETRY TO BE DESIGNED BY INTERIOR DESIGNER / CABINET MAKER. VERIFY w/ CABINET MAKER'S PLANS.
- NOTE 2:** UPON COMPLETION OF THE KITCHEN DESIGN, CONTRACTOR SHALL RETURN UPDATED PLANS TO THE ARCHITECT FOR ELECTRICAL COORDINATION AND REVISIONS.
- NOTE 3:** REMOVE EXISTING PLASTER AND GUT WALLS DOWN TO STUDS. PROVIDE NEW SISTER STUDS AND JOISTS ADJACENT TO EXISTING FRAMING AS REQUIRED TO ACHIEVE PLUMB, FLAT AND TRUE CONDITIONS AT ALL CABINET INSTALLATION SURFACES, INCLUDING FLOORS, WALLS AND CEILINGS.
- NOTE 4:** CONTRACTOR TO VERIFY THERE IS ENOUGH SPACE FOR 6" ABOVE THE KITCHEN COUNTER FOR BACKPLASH & HORIZONTAL OUTLETS. (PRADO OUTLETS RECOMMENDED. REFERENCE PHOTO BELOW)



SCHEMATIC 3D VIEW - ISO



SCHEMATIC 3D VIEW - KITCHEN



SCHEMATIC 3D VIEW - KITCHEN



INSPO PHOTOS

REMODEL EXISTING KITCHEN, REMOVE EXISTING CABINETS / STORAGE, APPLIANCES, LIGHT FIXTURES, PLUMBING FIXTURES AND ALL ASSOCIATED COMPONENTS

DEMO EXISTING STAIRS

REPLACE ENTRY DOOR

1 Existing - First Floor
1/4" = 1'-0"

CONTRACTOR TO VERIFY THERE IS MIN. 6" SPACE ABOVE THE KITCHEN COUNTER FOR HORIZONTAL OUTLETS

HOOD VENTILATION TO EXTERIOR. INSTALL MAKE UP AIR DAMPER IF HOOD IS OVER 400 CFM

FINAL CABINETRY TO BE DESIGNED BY INTERIOR DESIGNER - VERIFY w/ CABINET MAKER'S PLANS.

2 Proposed - First Floor.
1/4" = 1'-0"

REVISIONS	BY

Courtney Rombough A.I.A. LLC
ARCHITECT

ARCHITECT'S ADDRESS : 141 Central Ave. Montclair, NJ
PHONE: 973.985.8230
WEBSITE: COURTNEYROMBOUGH.COM
EMAIL: COURTNEY@COURTNEYROMBOUGH.COM

COURTNEY ROMBOUGH A.I.A. LLC
RA #21A02047700
08.13.2026

GARRIGAN JULIA & JACK
261 GROOVE STREET
MONTCLAIR, NEW JERSEY 07042
BLOCK 4512 - LOT 22

DRAWN	CHECKED
DATE	08.13.2026
SCALE	1/4" = 1'-0"
JOB	
DWG	
SHEET	

A-1

WALL LEGEND

-  = EXISTING WALL
-  = NEW 2x WOOD FRAME @ 16" O.C. WALL w/ 1/2" GYPBOARD ON EITHER SIDE
-  = EXISTING WALL TO BE DEMOLISHED

CONSTRUCTION LEGEND

1. DO NOT SCALE DRAWINGS.
2. ALL DIMENSIONS SHALL BE FIELD VERIFIED AND ANY DISCREPANCIES SHALL BE REPORTED PRIOR TO COMMENCEMENT OF WORK.
3. REFER TO GENERAL NOTES FOR ADDITIONAL INFORMATION.

GENERAL NOTES

1. FOR BEDROOMS:
VERIFY IN THE FIELD THAT AT LEAST ONE WINDOW PER ROOM MEETS EGRESS WINDOW REQUIREMENTS. IF NOT, THE CONTRACTOR MUST NOTIFY THE ARCHITECT AND OWNERS TO DECIDE ON REPLACEMENT WITH NEW EGRESS WINDOWS TO COMPLY WITH CODE.

2. EXISTING FINISHES
EX EXTERIOR FINISH TO BE REMOVED WHERE REQUIRED TO MEET PROPOSED ADDITION. STRUCTURE AND INSULATION TO REMAIN. REUSE EXTERIOR FINISH WHERE APPLICABLE.

3. EXISTING WINDOWS GLASS
IF NOT ALREADY TEMPERED, EX WINDOWS TO HAVE CATEGORY II IMPACT-RESISTANT SAFETY GLAZING FILM APPLIED, PER CPSC 16 CFR 1201 CATEGORY II STANDARDS.VERIFY GLAZING REQUIREMENTS FOR WINDOWS IN BATHROOMS, STAIRWAYS, BENCHES, AND ANY WINDOWS WITH SILLS LOWER THAN 24 INCHES.

REVISIONS	BY

Courtney Rombough A.I.A. LLC

ARCHITECT

ARCHITECT'S ADDRESS : 141 Central Ave. Montclair, NJ
PHONE: 973.985.8230
WEBSITE: COURTNEYROMBOUGH.COM
EMAIL: COURTNEY@COURTNEYROMBOUGH.COM

COURTNEY ROMBOUGH A.I.A. LLC
RA #21A02047700
08.13.2026



GARRIGAN JULIA & JACK

261 GROOVE STREET
MONTCLAIR, NEW JERSEY 07042
BLOCK 4512 - LOT 22


DRAWN	CHECKED
DATE	08.13.2026
SCALE	1/4" = 1'-0"
JOB	
DWG	
SHEET	

A-2

ALL DRAWINGS AND WRITTEN MATERIAL APPEARING HEREIN CONSTITUTE ORIGINAL AND UNPUBLISHED WORK OF THE ARCHITECT/ENGINEER AND MAY NOT BE DUPLICATED, USED OR DISCLOSED WITHOUT WRITTEN CONSENT OF THE ARCHITECT/ENGINEER.

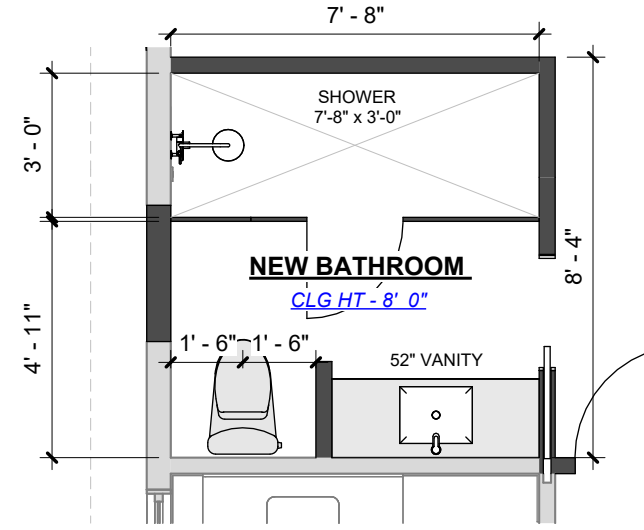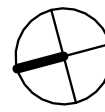


3 Proposed - Second floor OP#B
1/4" = 1'-0"

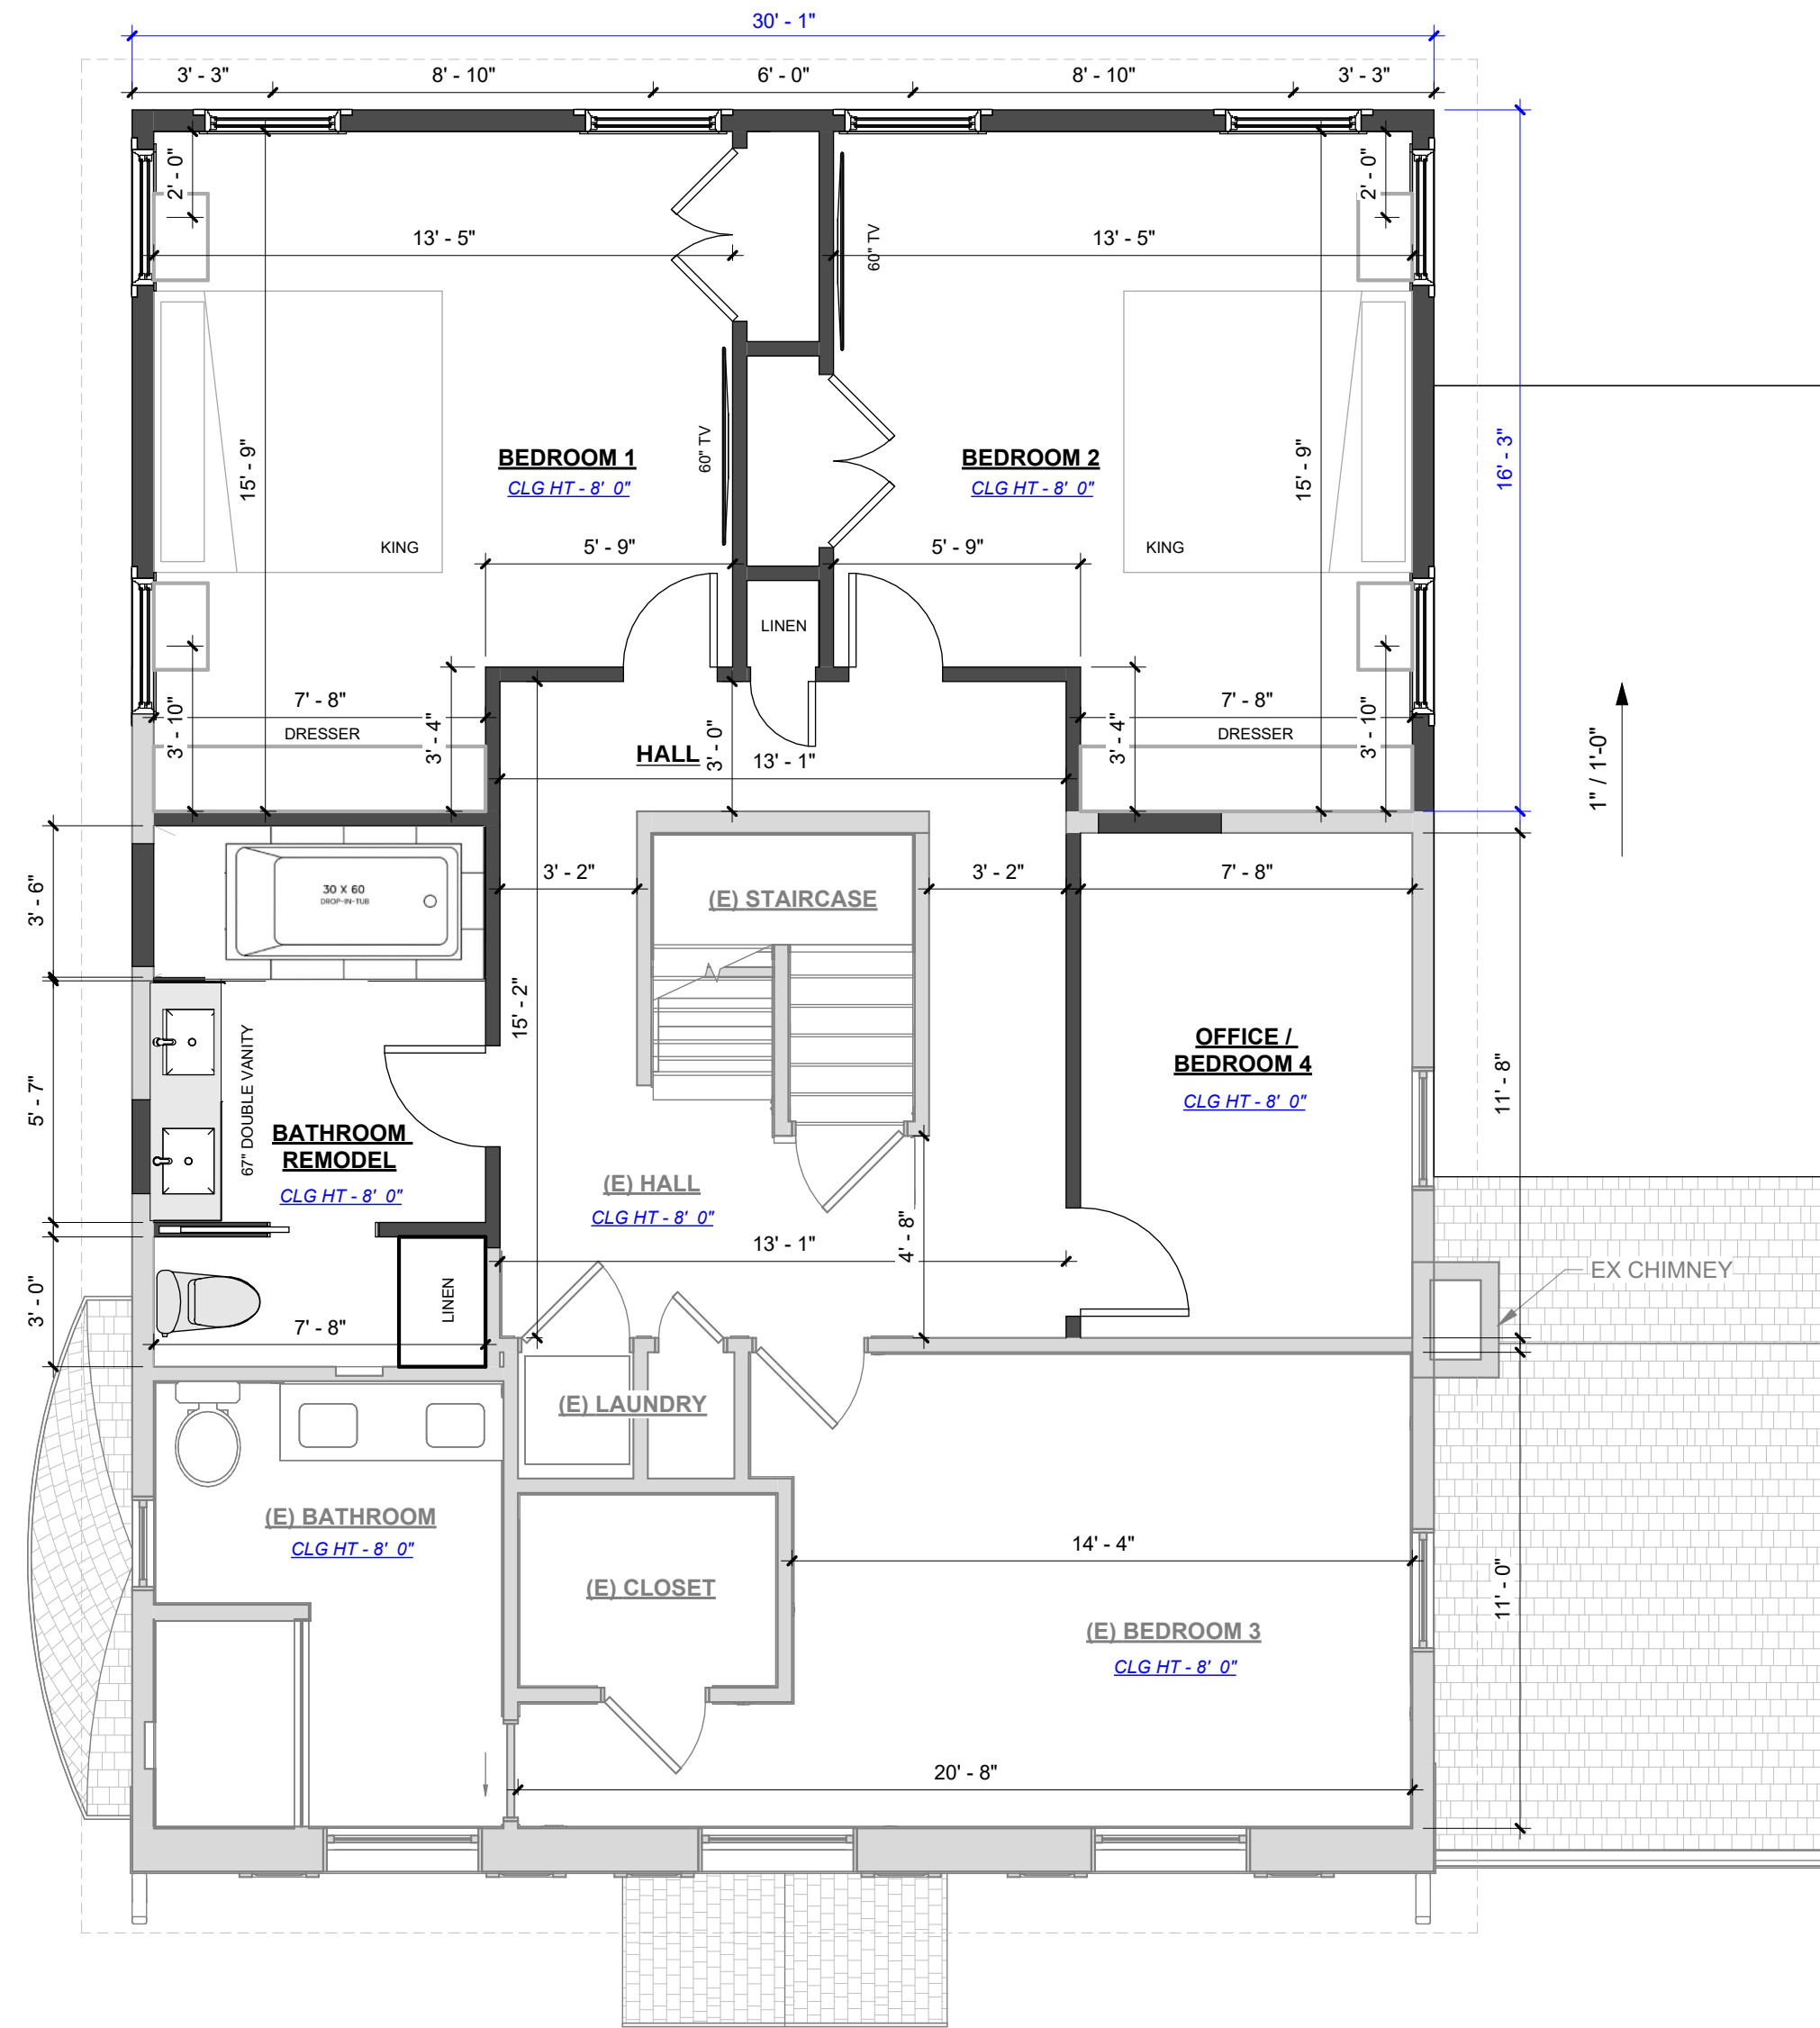

2 Proposed - Second floor.
1/4" = 1'-0"

REMODEL EXISTING BATHROOM,
REMOVE EXISTING CABINETS /
STORAGE, APPLIANCES, LIGHT
FIXTURES, PLUMBING FIXTURES AND
ALL ASSOCIATED COMPONENTS

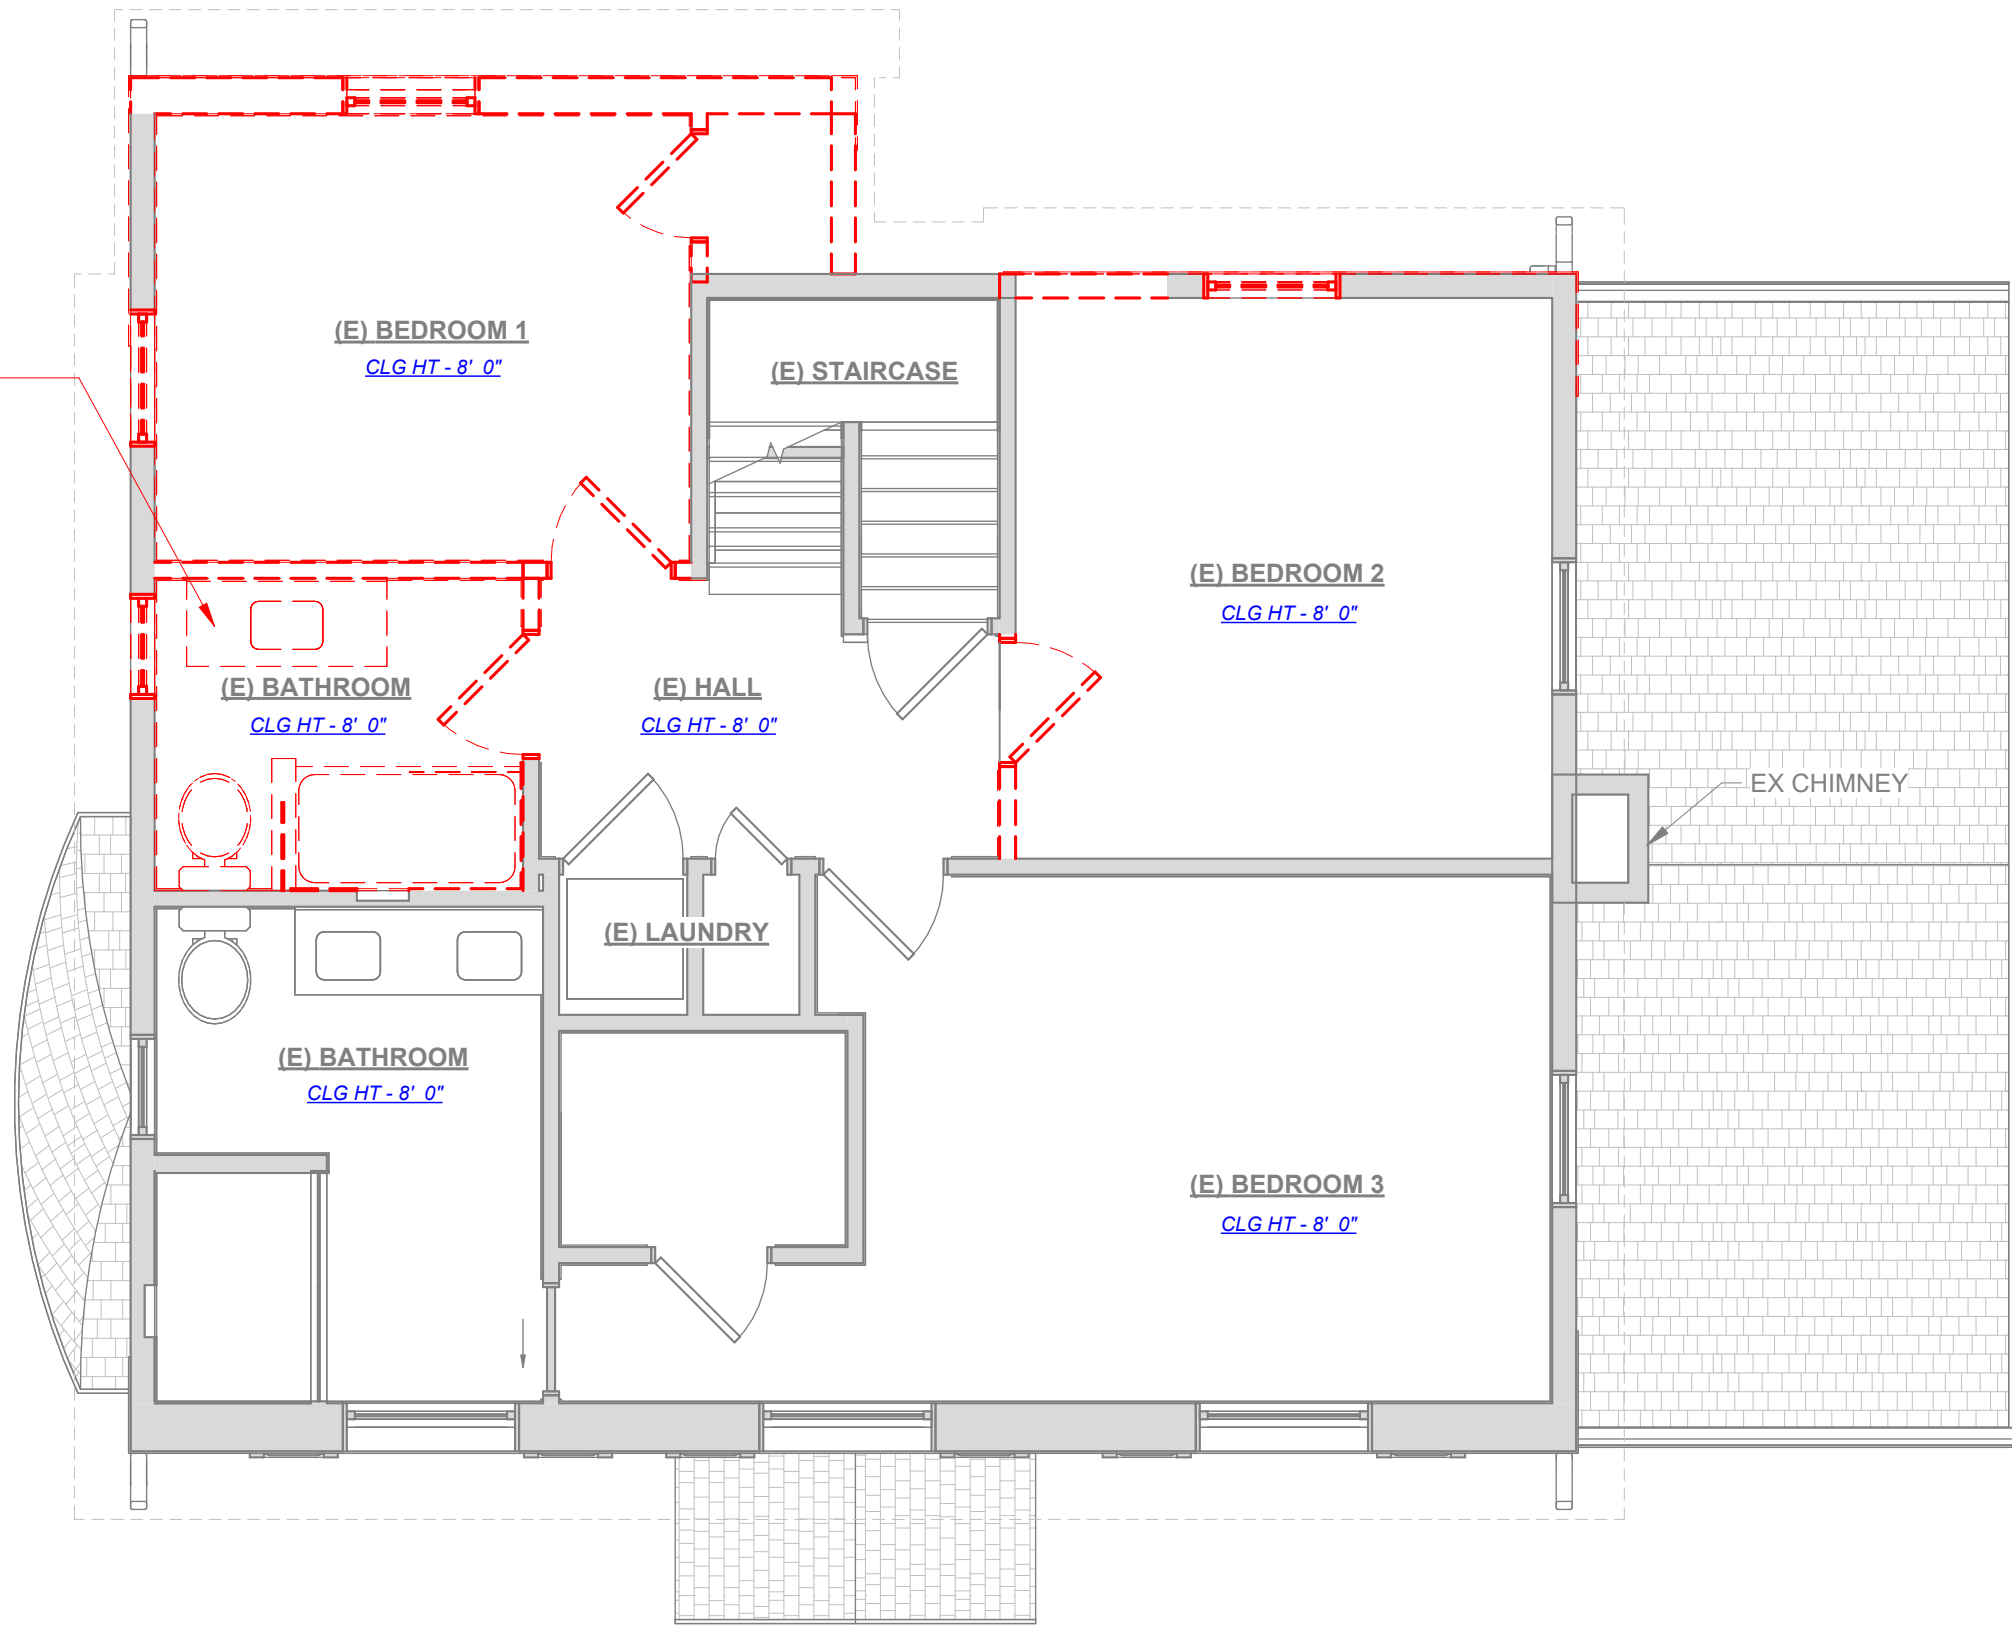






1 Existing - Second floor
1/4" = 1'-0"

WALL LEGEND


-  = EXISTING WALL
-  = NEW 2x WOOD FRAME @ 16" O.C. WALL w/ 1/2" GYPBOARD ON EITHER SIDE
-  = EXISTING WALL TO BE DEMOLISHED

CONSTRUCTION LEGEND

1. DO NOT SCALE DRAWINGS.
2. ALL DIMENSIONS SHALL BE FIELD VERIFIED AND ANY DISCREPANCIES SHALL BE REPORTED PRIOR TO COMMENCEMENT OF WORK.
3. REFER TO GENERAL NOTES FOR ADDITIONAL INFORMATION.

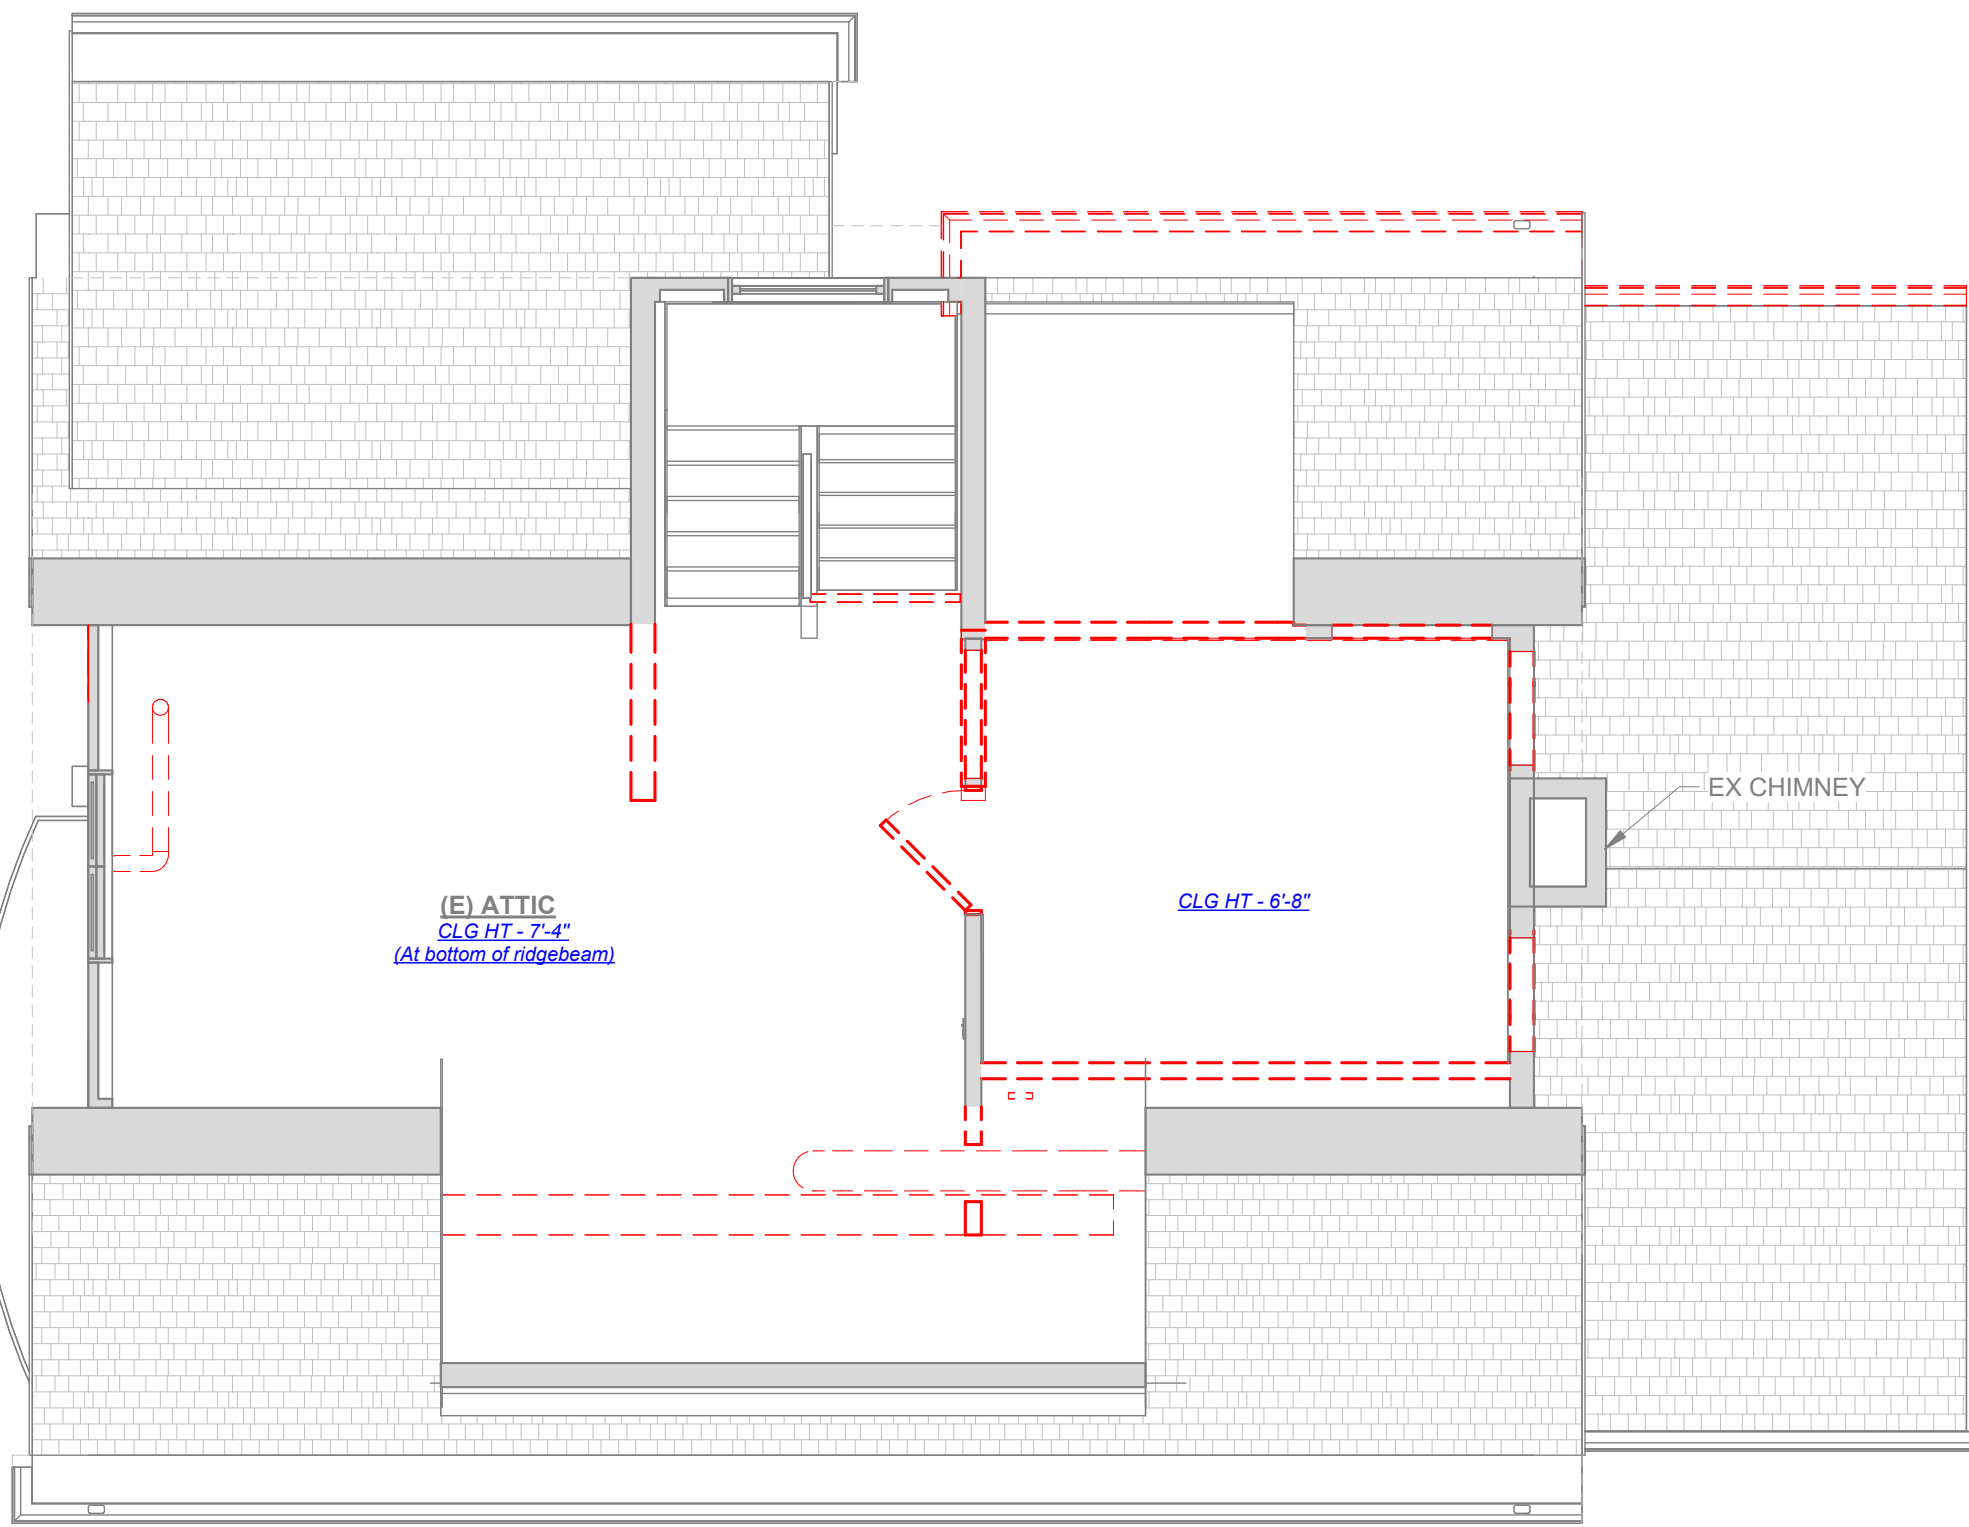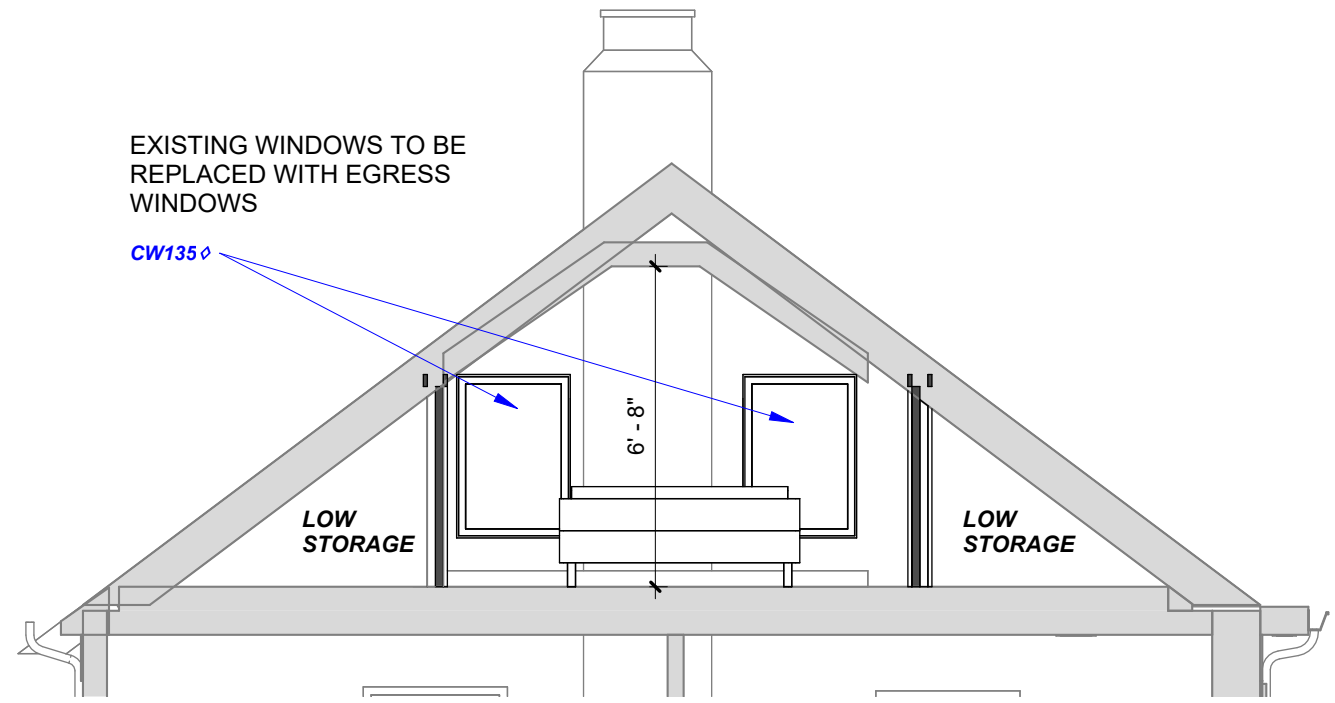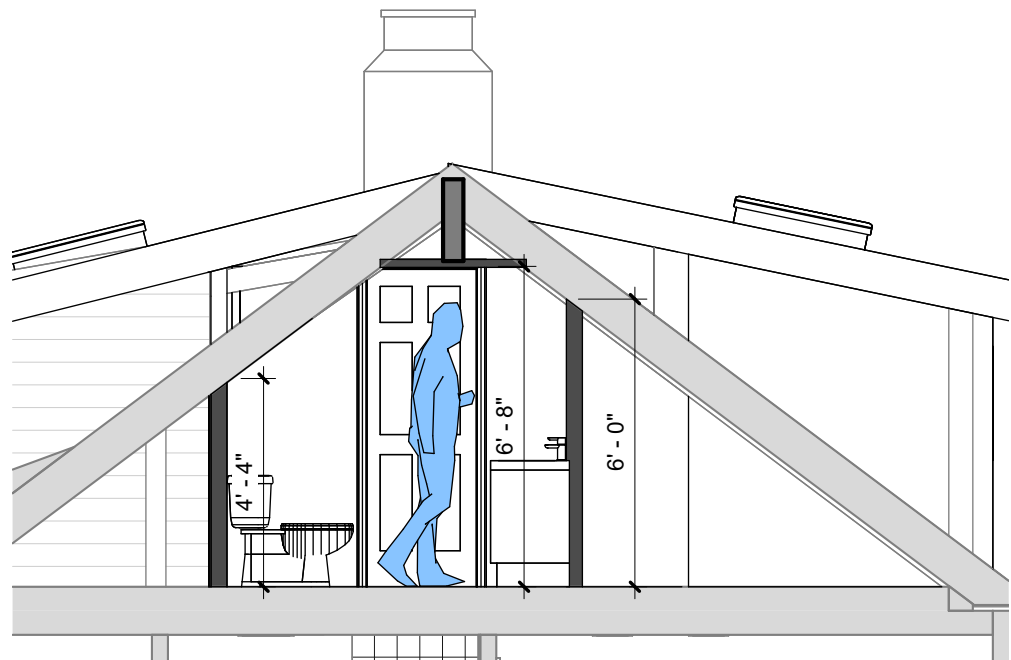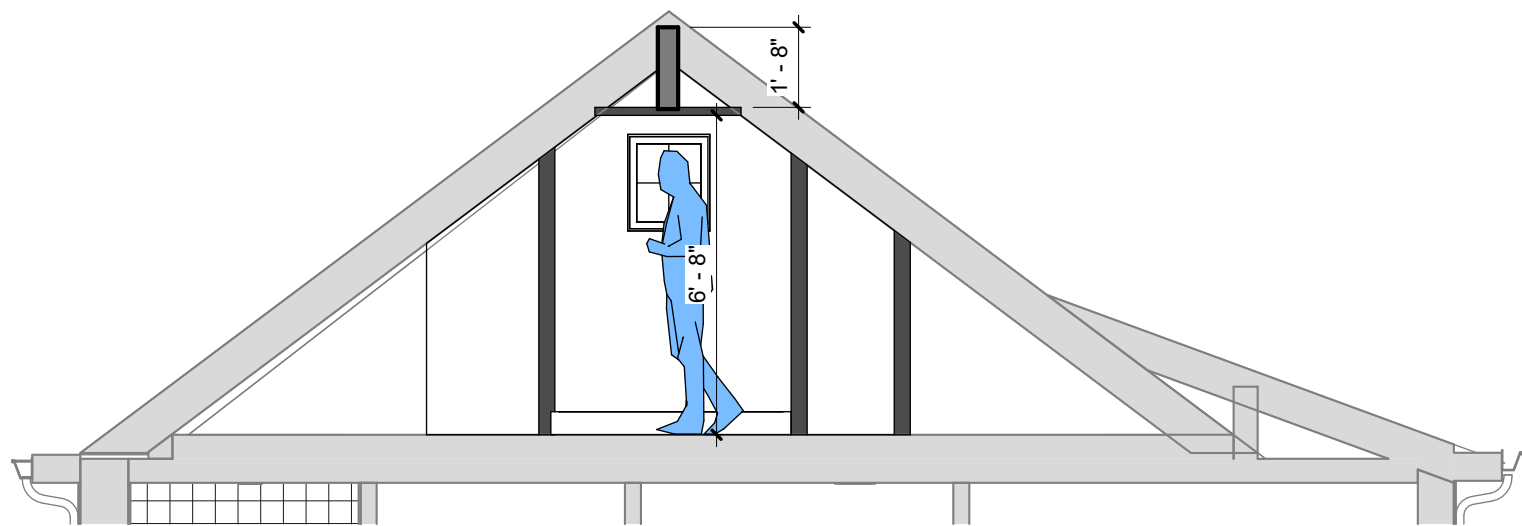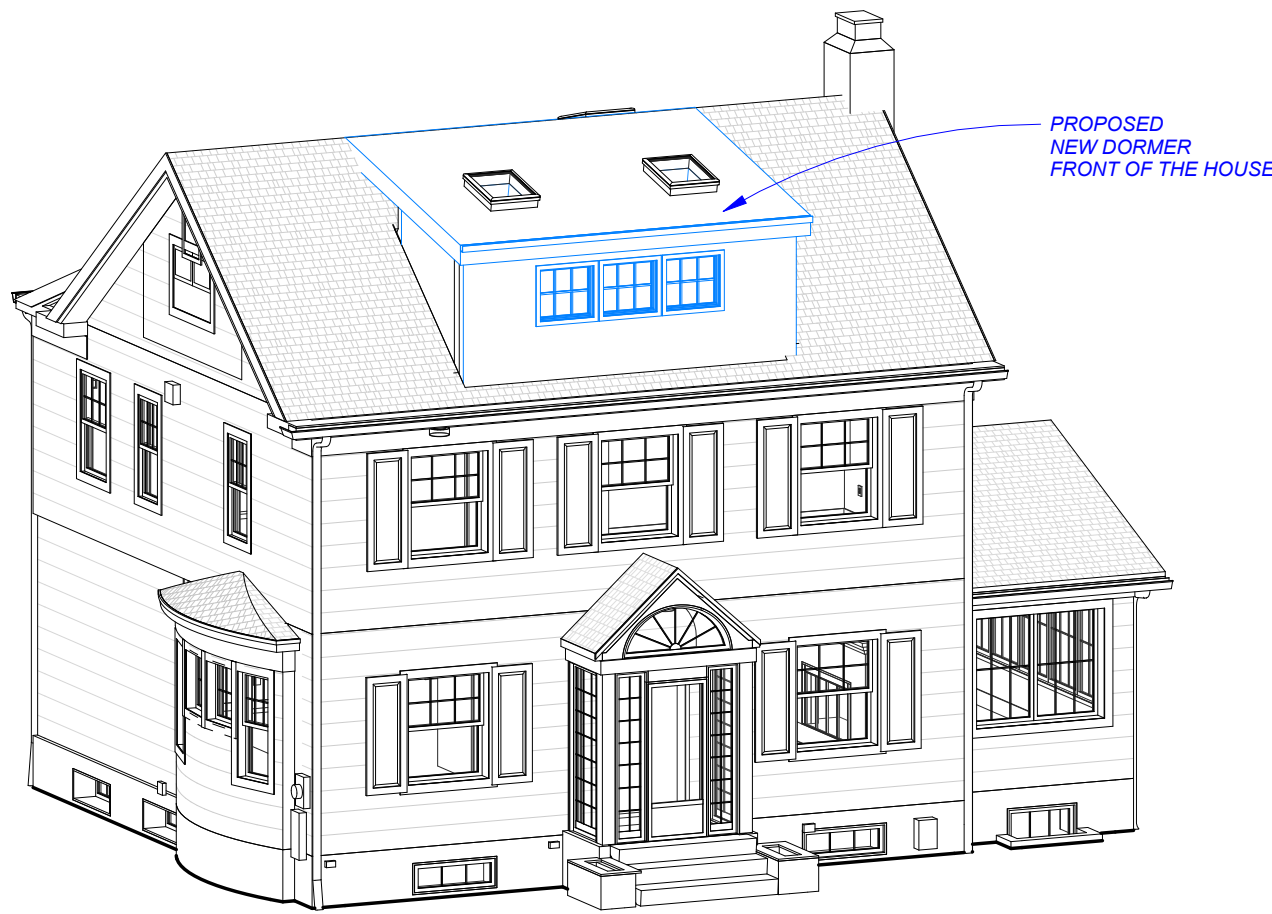

1 Existing - Third floor
1/4" = 1'-0"

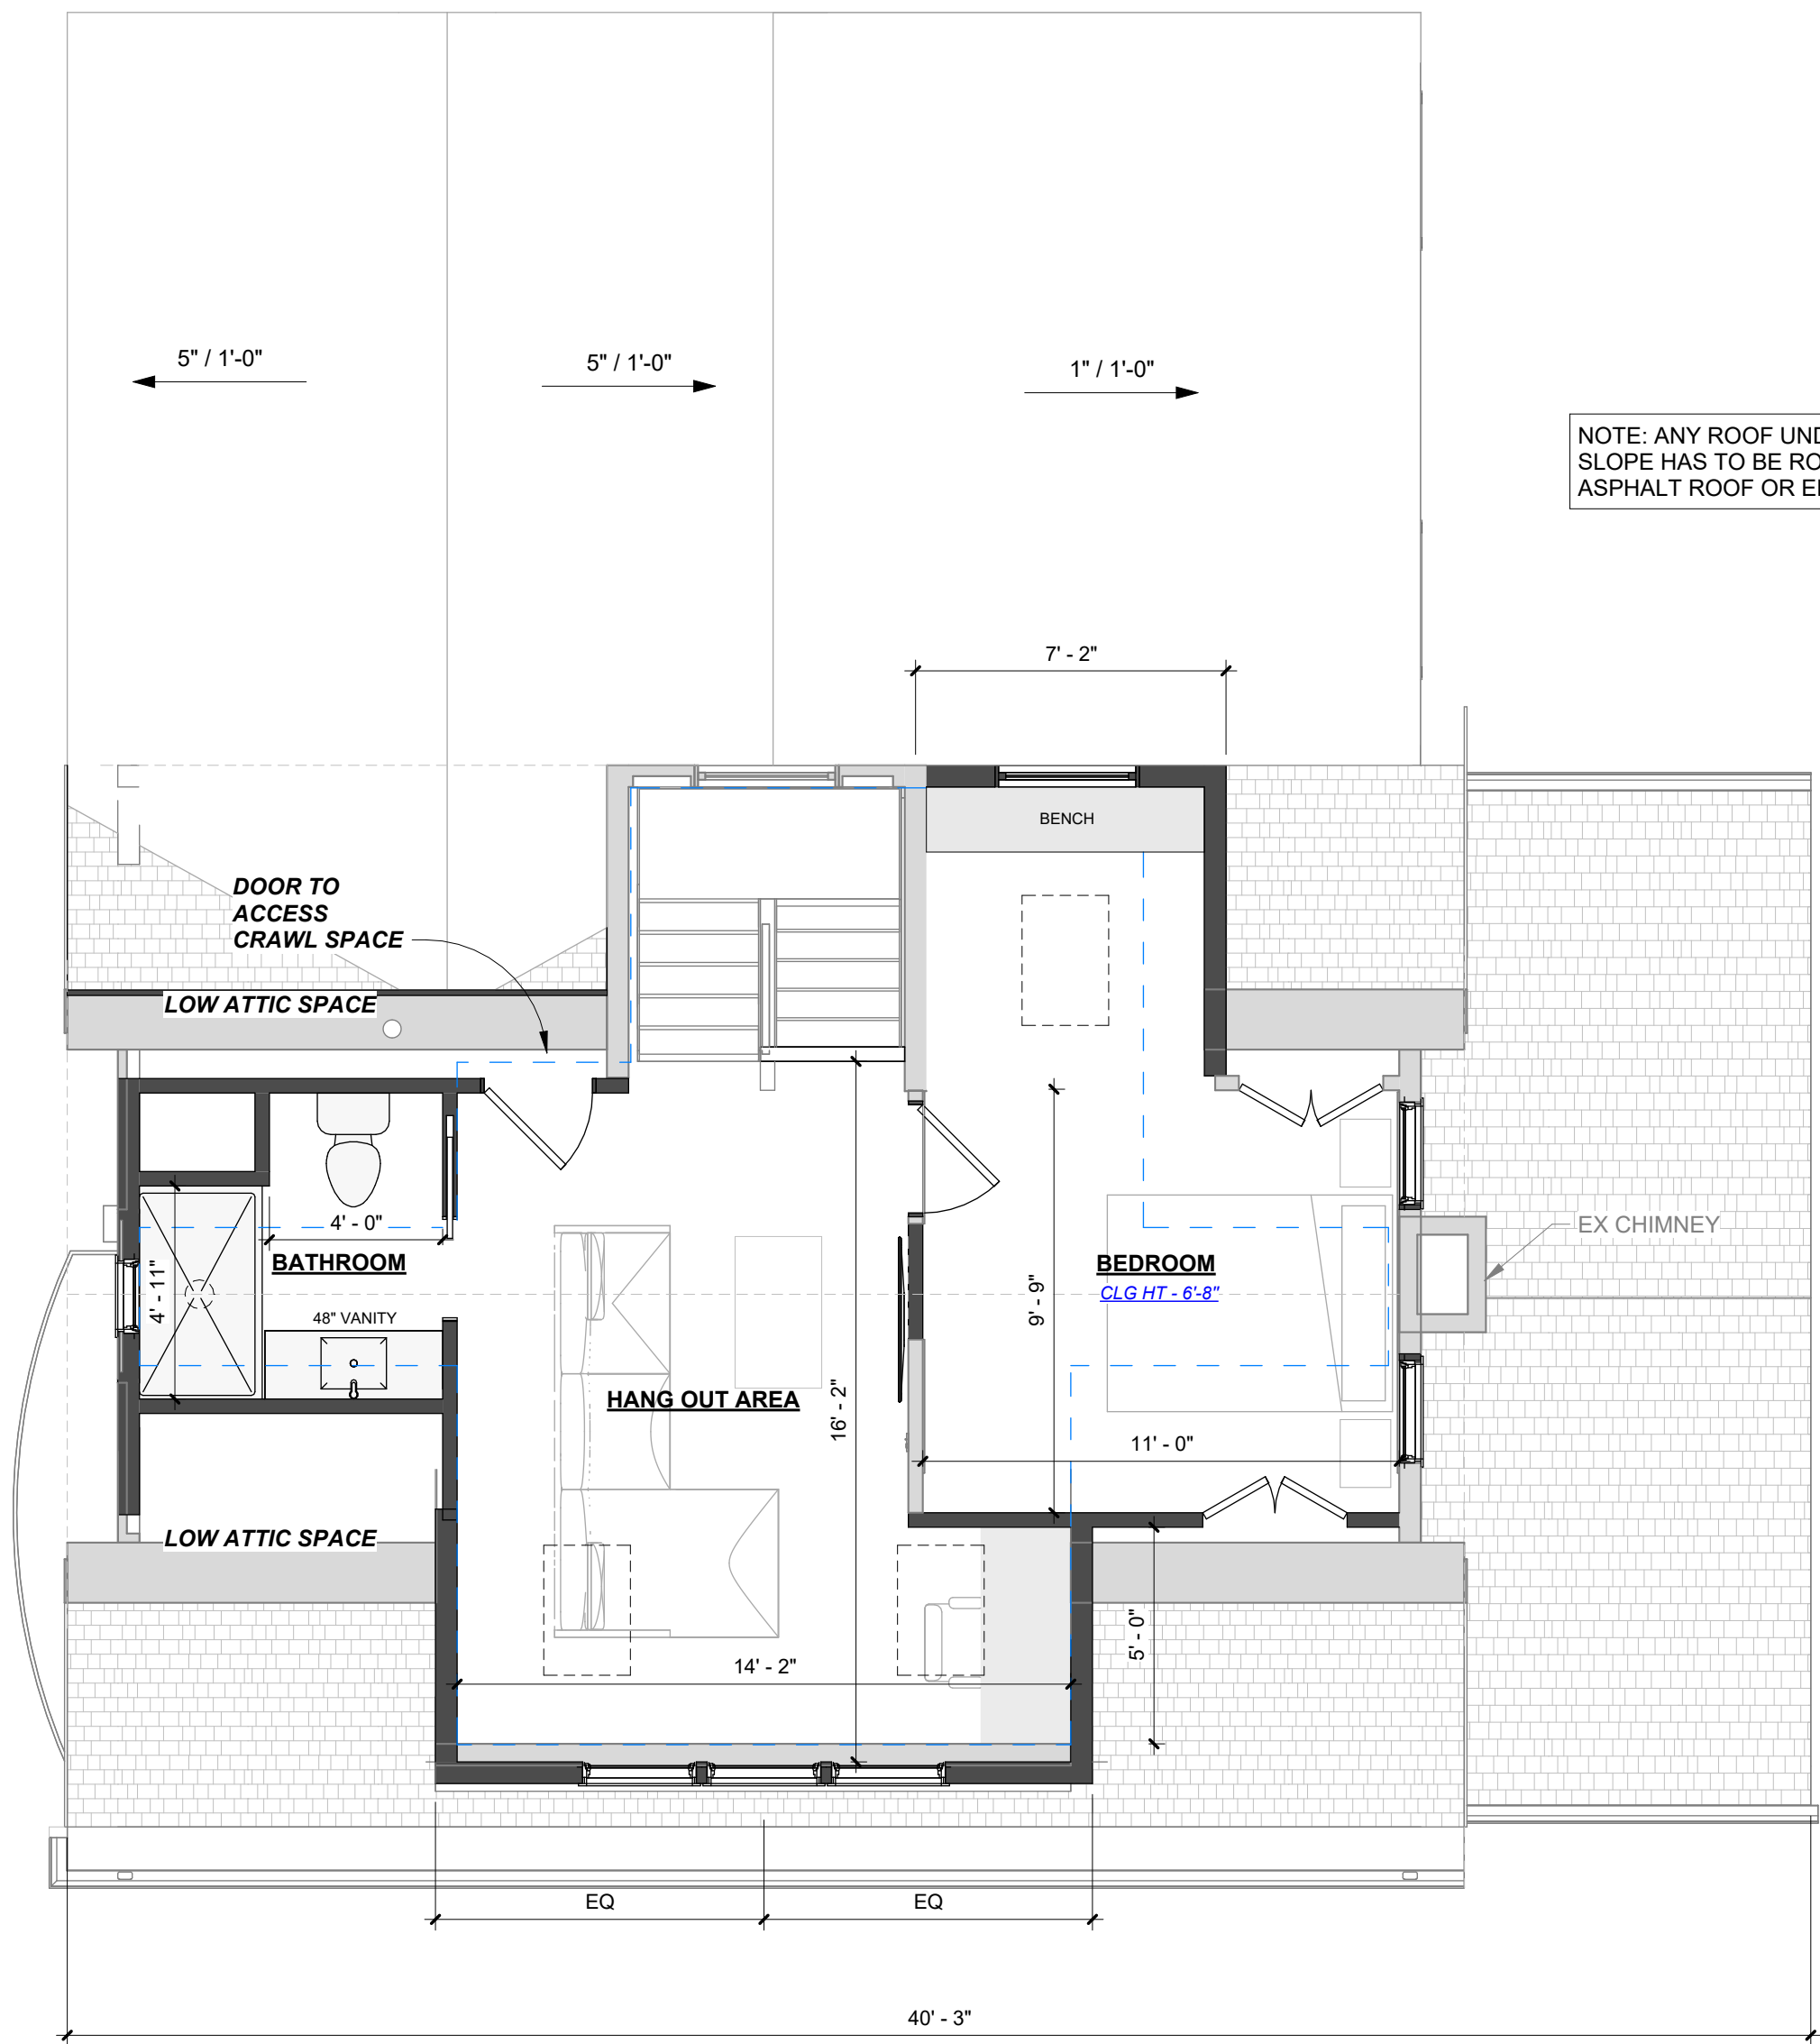

2 Poposed - Third floor
1/4" = 1'-0"

REVISIONS	BY

Courtney Rombough A.I.A. LLC
ARCHITECT

ARCHITECT'S ADDRESS : 141 Central Ave. Montclair, NJ
PHONE: 973.985.8230
WEBSITE: COURTNEYROMBOUGH.COM
EMAIL: COURTNEY@COURTNEYROMBOUGH.COM

COURTNEY ROMBOUGH A.I.A. LLC
RA #21A00047700
08.13.2026

GARRIGAN JULIA & JACK
261 GROOVE STREET
MONTCLAIR, NEW JERSEY 07042
BLOCK 4512 - LOT 22

DRAWN	CHECKED
DATE	08.13.2026
SCALE	1/4" = 1'-0"
JOB	
DWG	
SHEET	