

WALL LEGEND



-  = EXISTING WALL
-  = NEW 2x WOOD FRAME @ 16" O.C. WALL w/ 1/2" GYPBOARD ON EITHER SIDE
-  = EXISTING WALL TO BE DEMOLISHED

CONSTRUCTION LEGEND


1. DO NOT SCALE DRAWINGS.
2. ALL DIMENSIONS SHALL BE FIELD VERIFIED AND ANY DISCREPANCIES SHALL BE REPORTED PRIOR TO COMMENCEMENT OF WORK.
3. REFER TO GENERAL NOTES FOR ADDITIONAL INFORMATION.




REVISIONS	BY

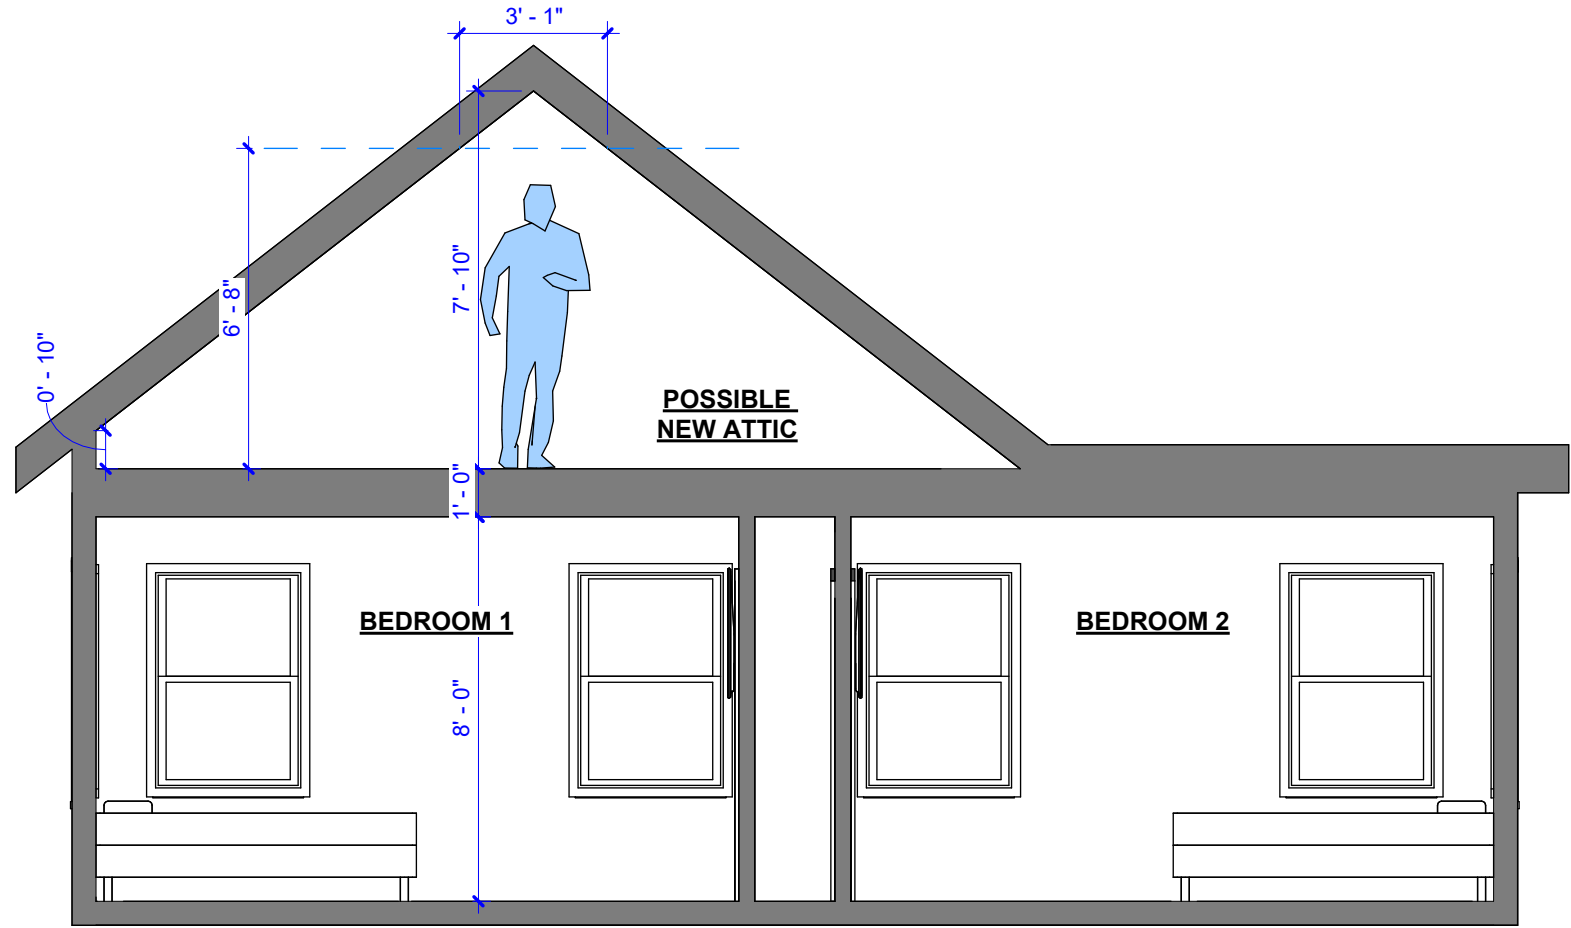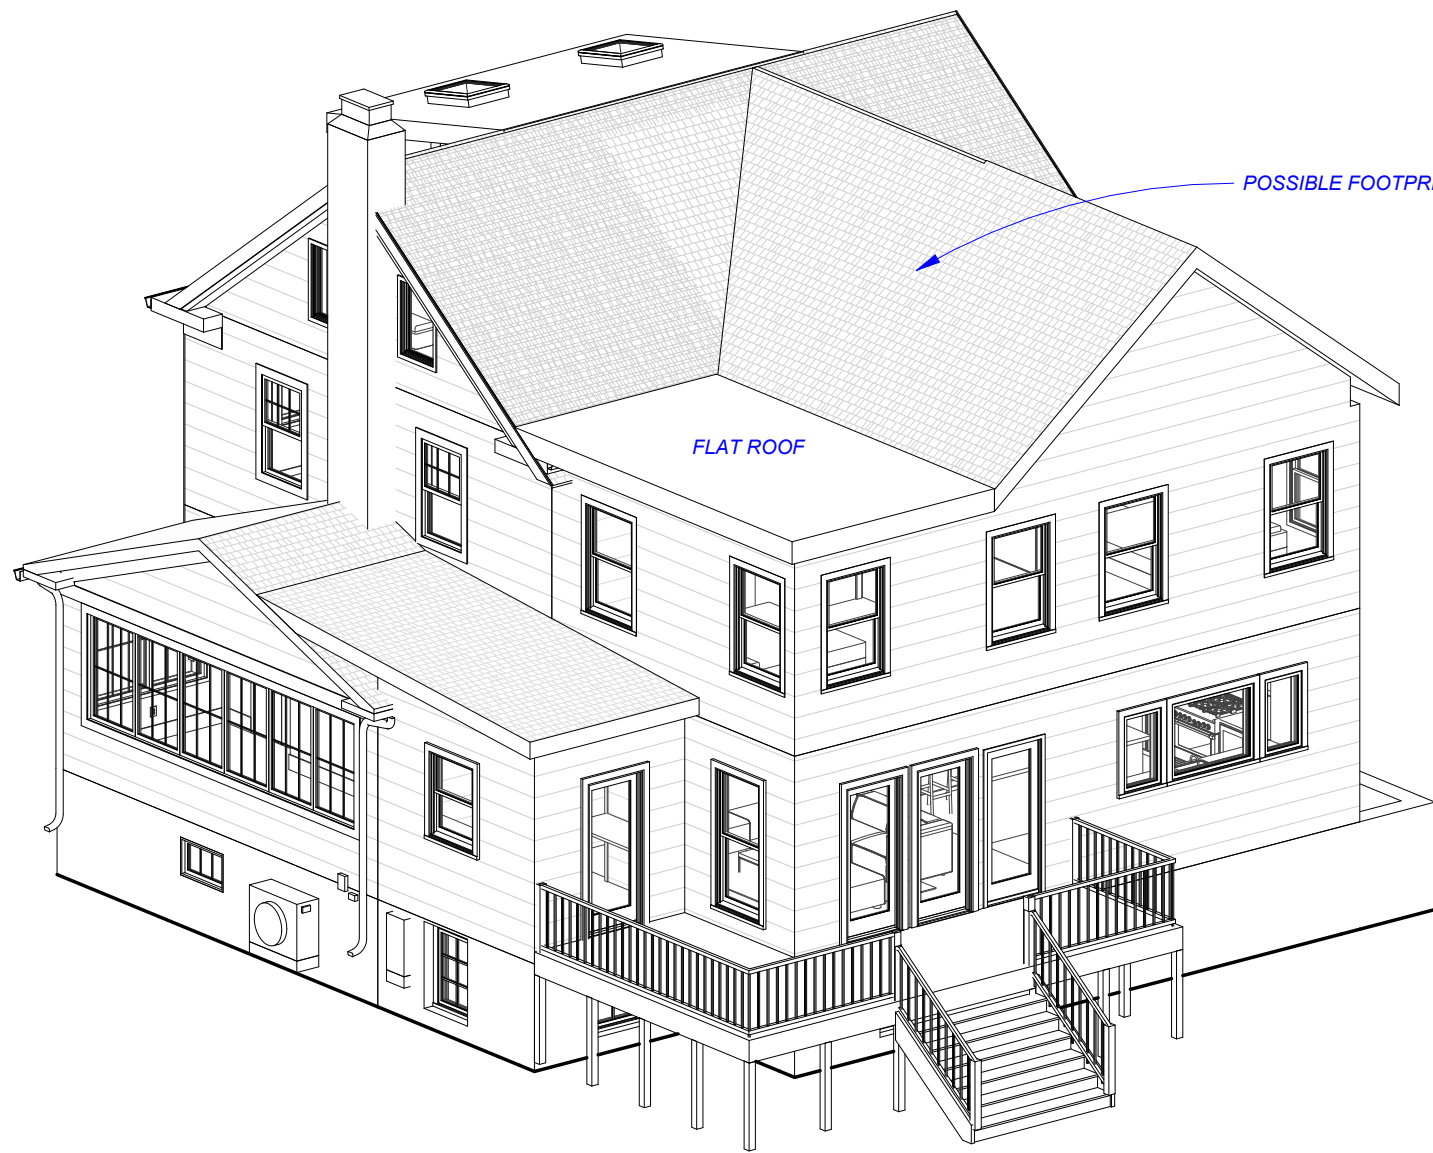

3 Building Section - OP #B
1/4" = 1'-0"

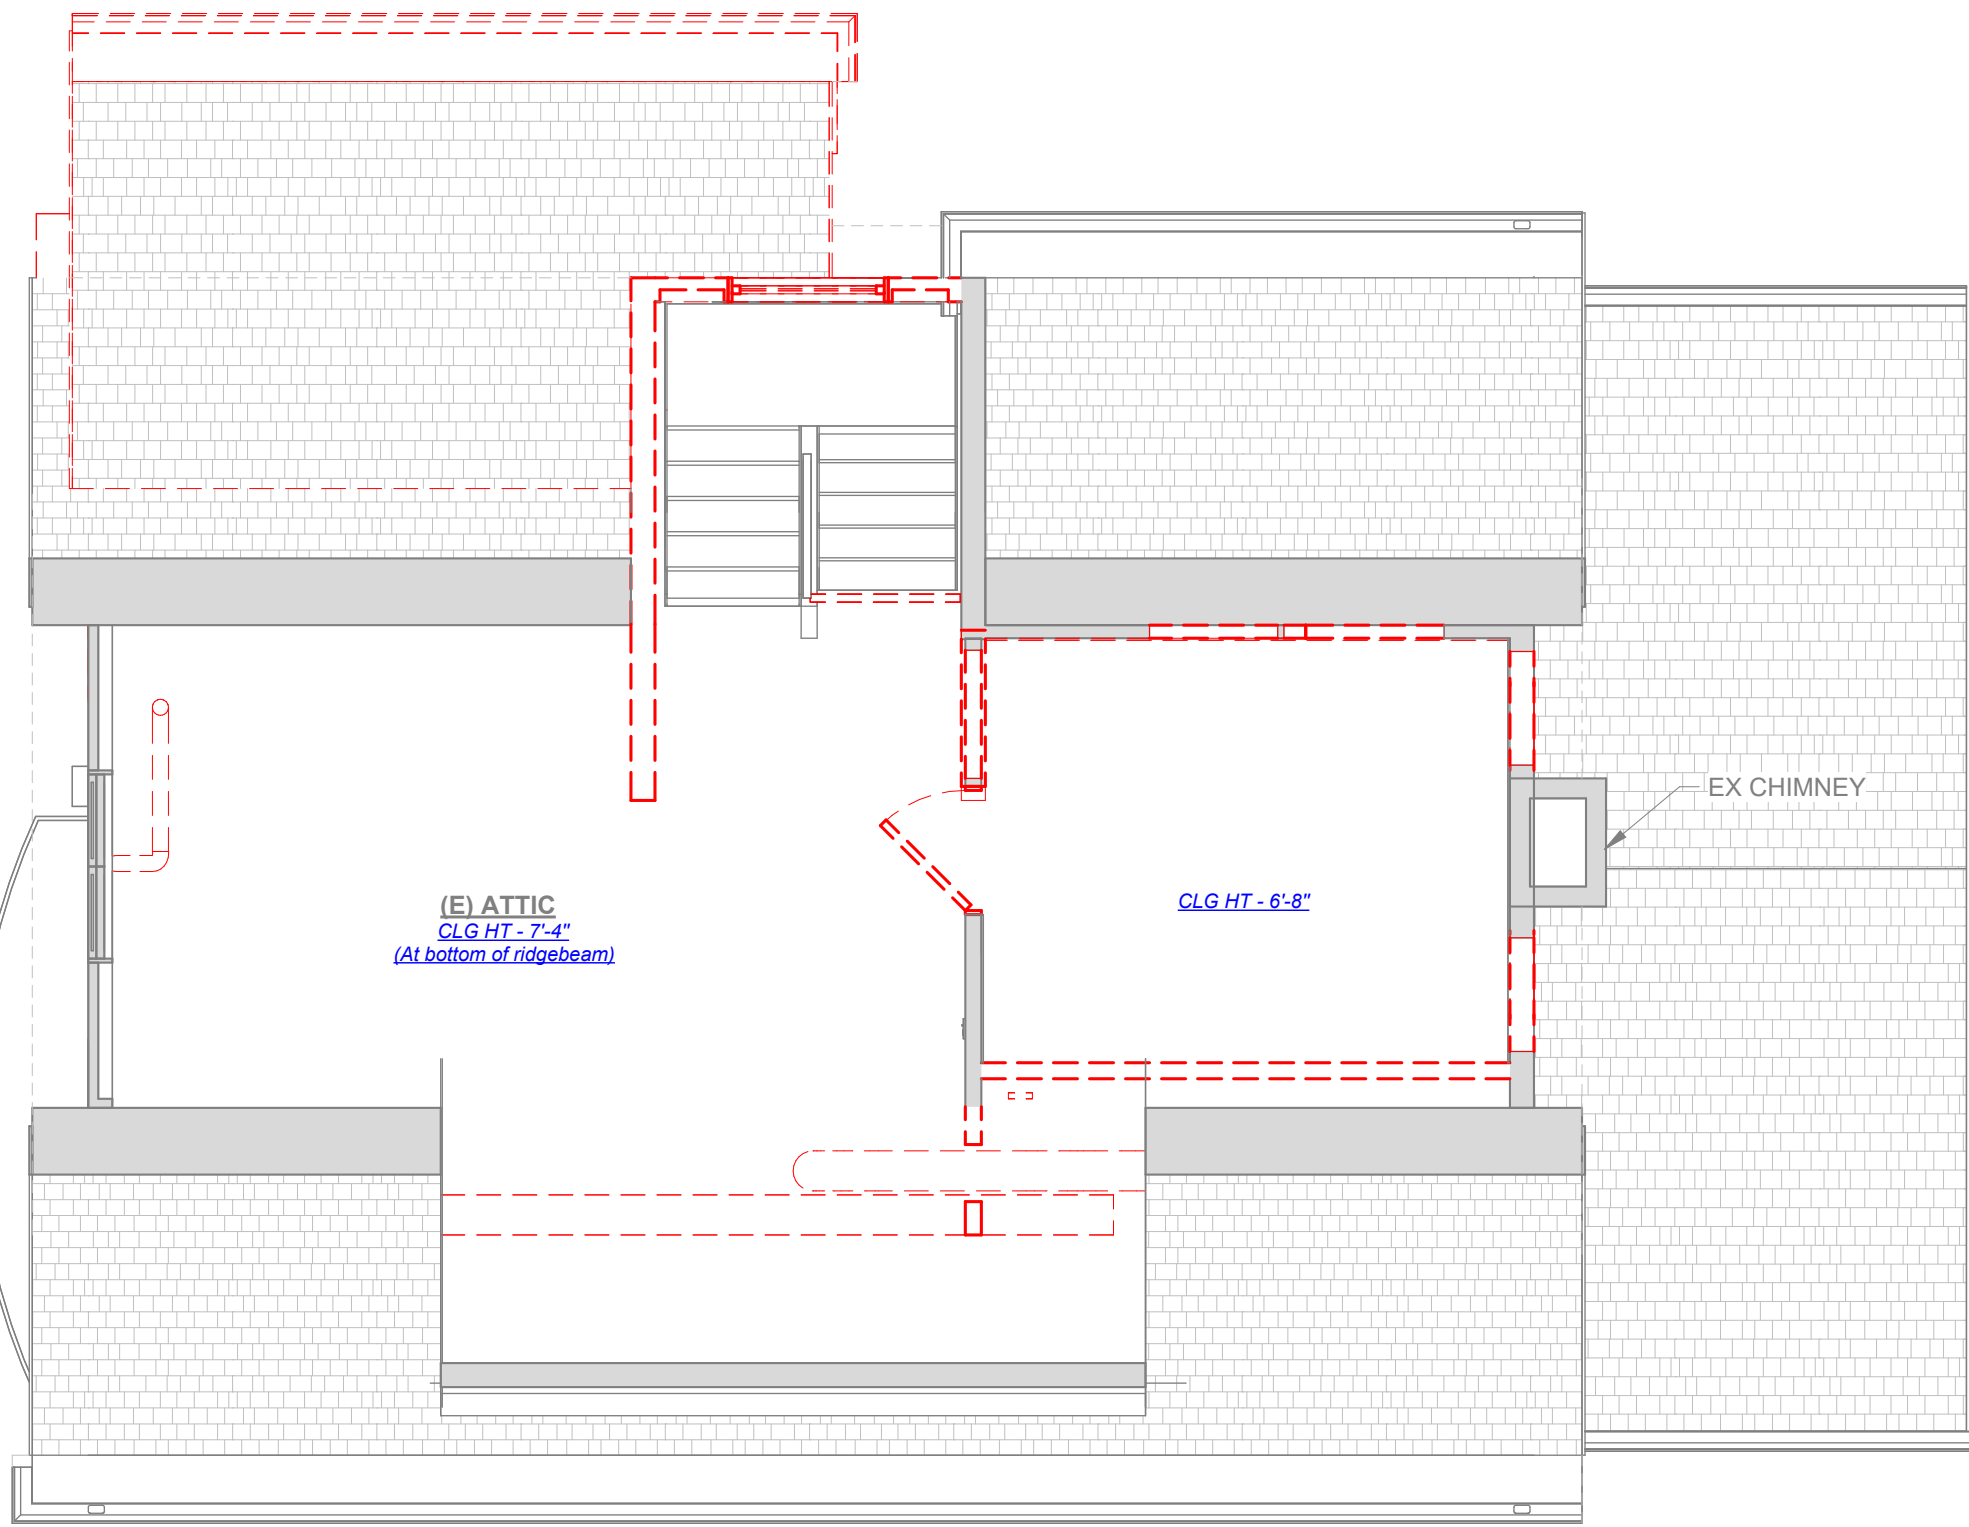

1 Existing - Third floor Copy 3
1/4" = 1'-0"

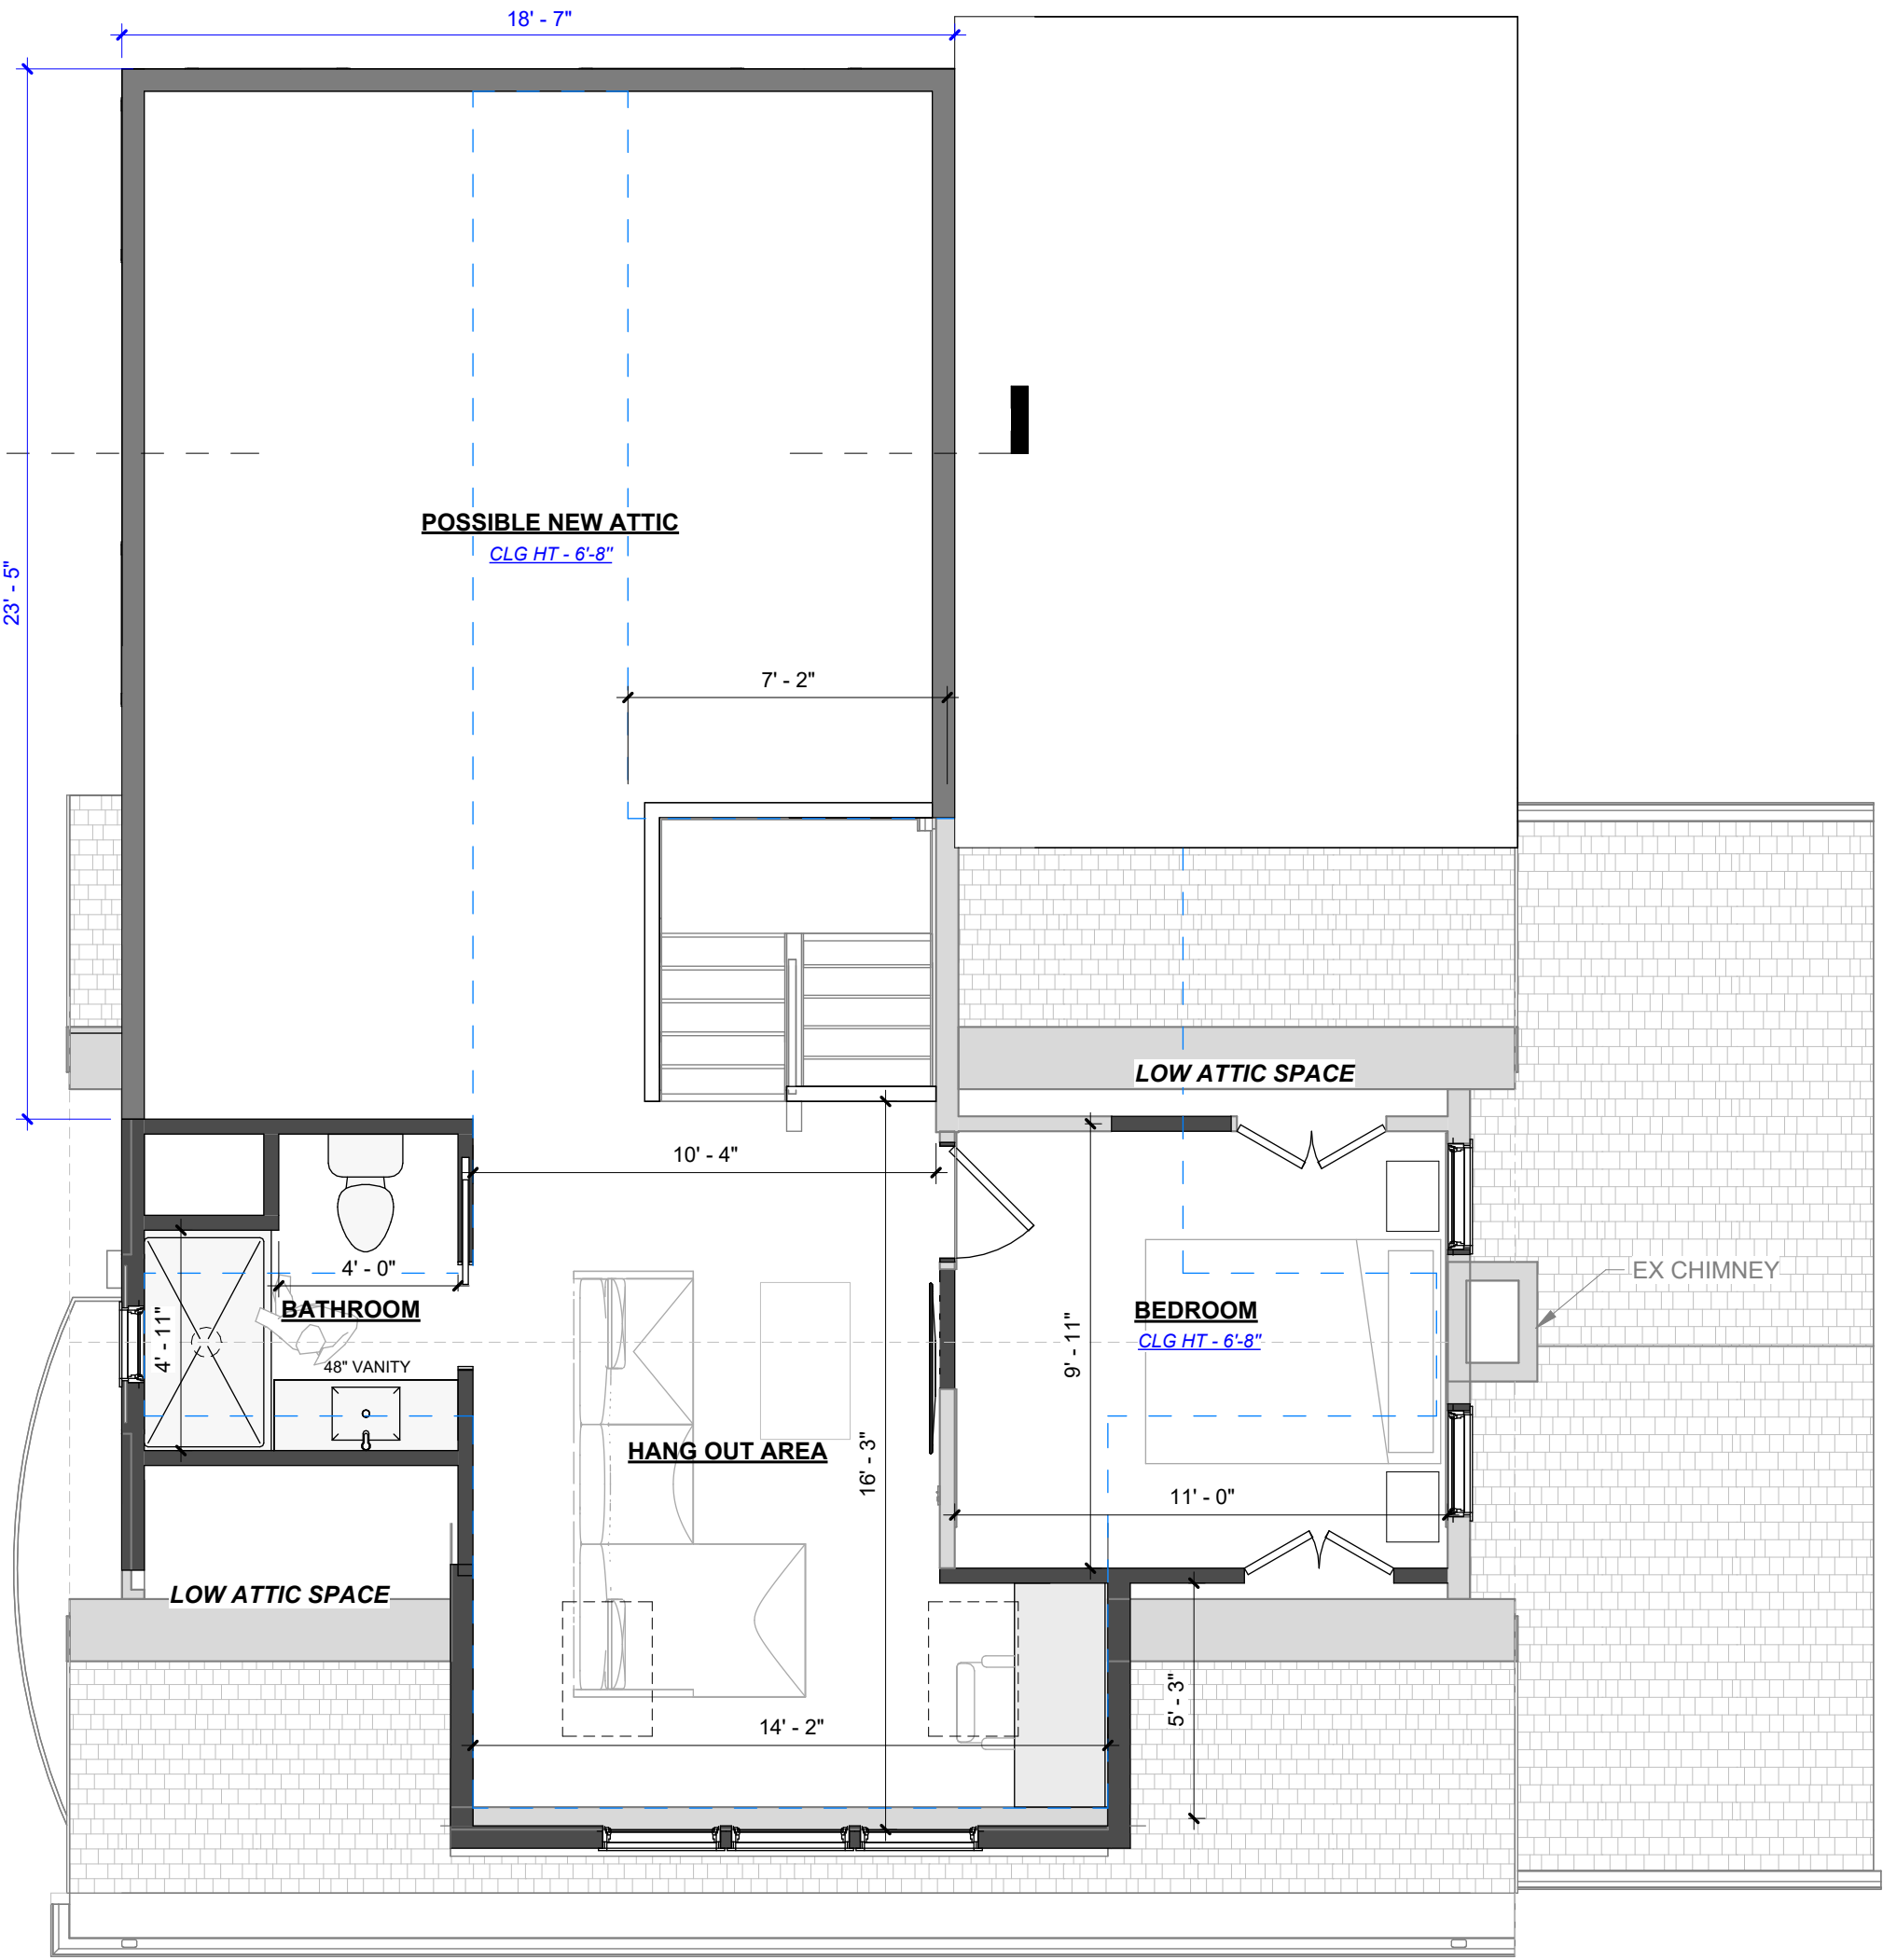

2 Proposed - Third floor Copy 1
1/4" = 1'-0"

Courtney Rombough A.I.A. LLC

ARCHITECT

ARCHITECT'S ADDRESS : 141 Central Ave. Montclair, NJ
PHONE: 973.985.8230
WEBSITE: COURTNEYROMBOUGH.COM
EMAIL: COURTNEY@COURTNEYROMBOUGH.COM

GARRIGAN JULIA & JACK

261 GROOVE STREET
MONTCLAIR, NEW JERSEY 07042
BLOCK 4512 - LOT 22

DRAWN	CHECKED
DATE	08.13.2026
SCALE	1/4" = 1'-0"
JOB	
DWG	
SHEET	

A-3
OP#B